Small Wood Cabin

Sheet Index	
Layout ID	**Layout Name**
A.01.1	Cover
A.01.2	Wall types
A.01.3	Legal
A.02.1	Foundation Plan
A.02.2	Ground Plan
A.02.3	Roof Plan
A.03.1	South Elevation
A.03.2	North Elevation
A.03.3	East Elevation
A.03.4	West Elevation
A.04.1	S-01 Building Section
A.05.1	Bathroom & Kitchen Elevations
A.06	Windows and Doors Lists
A.07	Kitchen Cabinet

	Total Area: 734 sq ft
	Dimensions:41' L X 25' W X 20' H
	Bedroom's size: 14' L X 10' W X 9' H
	Patio: 2 Patios
	Acommendation: 1-3 People
	Bathroom: 1 bathroom with bathtub
	Kitchen: Eat in island kitchen
	Laundry: Laundry closet in the bathroom
	Utility: Outside detached from the house
	HVAC: Mini-split

Design with **FRANK**

Modern Cabin

THIS PLAN IS PROTECTED UNDER FEDRAL COPYRIGHT LAWS. ANY UNAUTHORIZED REPRODUCTION OR MODIFICATION OF THESE PLANS IS A VIOLATION OF COPYWRIGHT LAWS.

COPYRIGHT ALL RIGHTS RESERVED
DESIGN WITH FRANK.INC

Drawing Name
Cover

Drawing Scale

Layout ID
A.01.1

GENERAL PROJECT NOTES:

All house plans from Design with Frank are designed to comply with the International Residential Code (IRC).
Every state, county or municipality will have its own building code requirements. It is possible that your plan may need to be modified to comply with these local requirements. This is particularly true in coastal areas and those facing seismic events, extreme winds and heavy snow. If you are building in any of these areas, it is likely that a licensed structural engineer will be needed to provide the necessary calculations and additional drawings. We authorize the use of our plans conditioned on your obligation and agreement to strictly comply with all local building codes, ordinances, regulations and requirements, including permits and inspections at the time of and during construction. We recommend checking with your local building department for the most current requirements.
All pre-drawn plans from Design with Frank do not carry a stamp from a licensed architect. If this is a requirement from your local building department, you will need to hire an architect or engineer to review and stamp the plans.

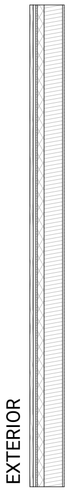

WALL-A
Total Width 10 1/4"

EXTERIOR
1" PINE VERTICAL SIDING
3/4" HORIZONTAL FURRING STRIP
2 1/2" ZIP PANEL WITH SHEATHING / AIR BARRIER
5 1/2" WOOD STUD/ CELLULOSE INSULATION
VAPOUR BARRIER
1/2" GYPSUM BOARD INSIDE
INTERIOR

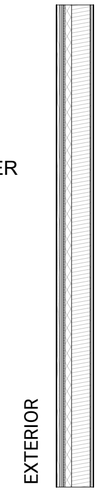

WALL-B
Total Width 10 3/4"

EXTERIOR
1" PINE VERTICAL SIDING
3/4" HORIZONTAL FURRING STRIP
2 1/2" Z PANEL WITH SHEATHING / AIR BARRIER
5 1/2" WOOD STUD/CELLULOSE INSULATION
VAPOUR BARRIER
1/4" CEMENT MORTAR.
3/4" TILE
INTERIOR

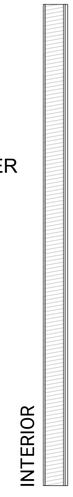

WALL-D
Total Width 7 1/4"

INTERIOR
1/2" GYPSUM BOARD
VAPOUR BARRIER
5 1/2" WOOD STUD.
VAPOUR BARRIER
1/2" CEMENT BACKER BOARD
3/4" TILE
BATHROOM

WALL-E
Total Width 6 1/2"

1/2" GYPSUM BOARD
5 1/2" WOOD STUD.
1/2" GYPSUM BOARD

Design with FRANK

Modern Cabin

THIS PLAN IS PROTECTED UNDER FEDRAL COPYRIGHT LAWS. ANY UNAUTHORIZED REPRODUCTION OR MODIFICATION OF THESE PLANS IS A VIOLATION OF COPYWRIGHT LAWS.

COPYRIGHT ALL RIGHTS RESERVED
DESIGN WITH FRANK.INC

Drawing Name
Wall types

Drawing Scale

Layout ID
A.01.2

LICENSE AGREEMENT FOR USE OF DRAWINGS AND SPECIFICATIONS

The undersigned licensee ("Licensee") desires to obtain from Design with FRANK. INC the right to obtain drawings and specifications to facilitate Licensee's construction of a single home, and Design with FRANK is willing to grant such right to Licensee on the terms and conditions set forth below, which both parties agree shall govern their rights, duties and obligations to each other with respect to the subject matter of this agreement ("License Agreement").

Therefore, in consideration of the foregoing, Design with FRANK.INC and Licensee agree as follows:

A. Use of Drawings and Specifications

1. These Drawings and Specifications (the "Plans") are the property of Design with FRANK.INC and are protected by United States Copyright Laws. Any use of the Information contained in the Plans beyond the one-time use authorized by a purchase of this License, or any duplication, publication, sale or distribution of any part of these Plans without prior written consent of Design with FRANK.INC is prohibited and represents a violation of federal laws subject to criminal and civil penalties.

2. A purchase of this License grants a limited license to the purchaser as "Licensee" to use such Plans to construct a single home in accordance with the terms hereof. These terms represent the License Agreement between Design with FRANK.INC and Licensee. Licensee acknowledges that all rights of ownership, title, and interest in the copyrights, Plans, and derivative works remain with Design with FRANK.INC, or if derivative works are created by Licensee or its builder or architect after Licensee's purchase, the rights therein are hereby transferred by Licensee to Design with FRANK.INC. Modified plans are considered derivative works of the original and receive the same copyright protection even if completely redrawn. This License for use of the Plans ends with the completion of the house or abandonment of the construction project for which the License was acquired. This limited License is personal to Licensee, and Licensee acknowledges that the Plans and License are not transferable to a third party.

3. Any use of the Plans or modifications of the Plans, by the Licensee's builder or others is done at Licensee's own risk. Licensee should have the Plans reviewed by a local licensed architect and engineer before the start of construction. The information contained within the Plans is to indicate design intent and basic construction detailing. It is the Licensee's builder's responsibility to provide standard construction details and practices, to create a structurally sound and weatherproof finished project.

B. Content of Plans

1. These Plans do not include detailed electrical, plumbing, heating or air conditioning drawings due to the wide variety of local codes and climatic conditions. Licensee is advised to have a local electrical engineer, mechanical engineer, or builder provide detailed electrical, plumbing, heating or air conditioning drawings as may be required for permits and construction. The floor plan and associated details are provided as a basic guide for a typical slab on grade/poured concrete foundation system. Licensee should have a local licensed architect or engineer provide a site-specific foundation design as necessary.

2. These Plans provide ideas and concepts and are not intended to be complete in all respects and details. Variations in standard sizes of window and door brands and types and use of different materials and thicknesses can change details. Varying local codes, ordinances, regulations, foundation requirements, and the layout of electrical, mechanical, and plumbing systems may also dictate that certain details be changed in order to comply therewith.

3. The qualifications and limitations contained in the Specifications attached to the Plans are incorporated herein by reference.

A. Licensee's and its Builder's Responsibilities

1. It is the responsibility of the Licensee and its builder to ensure that:

(a) all construction is in accordance with the latest edition of all applicable National, State, and Local Building Codes.

(b) all construction is in accordance with the latest edition of all applicable construction standards, fire department standards, utility company standards, and best practices.

(c) all manufactured articles, material, and equipment are applied, installed, connected, erected, used, cleaned, adjusted, operated, and conditioned as directed by manufacturers, and that builder follows all instructions to maintain and preserve all expressed and implied warranties and guarantees.

(d) all materials, equipment, and components are new and of good quality.

(e) all dimensions and details are accurate and appropriate according to local conditions and that the final selection of materials such as masonry, floor joists, lumber, structural members, construction panels, roofing, etc. (all of which can create variations in dimensions and details) are consistent therewith.

(f) any changes or deviations from the Plans that are the result of such variances have been incorporated into and coordinated with the Plans.

(g) all tests and inspections as specified or otherwise required by the local building department have been coordinated and are timely obtained and all costs and fees for same have been paid.

(g) all building permits, and upon completion of the project, a Certificate of Occupancy, Use (or equivalent as local conditions require) from the applicable building department have been obtained.

(h) only State licensed contractors/subcontractors have been used for all plumbing and electrical work, and that they have been required to submit all required permits, certificates, and sign-offs to the Licensee for Licensee's records prior to final payment.

(i) all dimensions have been verified, and any discrepancies addressed prior to submission of construction proposal and beginning of work.

1. Plans may be scaled for estimating purposes only. For all dimensions and locations, refer to dimensions on Plans. It is the responsibility of the Licensee and its builder to verify all dimensions in the field.

2. The Licensee's builder shall be exclusively responsible for any warranty or guarantee required by the Licensee.

B. General

1. Any names of materials and manufacturers shown on these Plans do not represent an endorsement or recommendation by Design with FRANK.INC. Final selections of materials are the responsibility of the Licensee and Licensee's builder, including but not limited to proper installation of materials, nailing, gluing, caulking, insulating, flashing, weatherproofing and many other small items and details not necessarily indicated in the Plans, and over which Design with FRANK.INC has no control or responsibility. Design with FRANK.INC shall not be held liable for any errors, omissions, or deficiencies in any form.

2. THE PLANS ARE PROVIDED "AS IS" WITHOUT REPRESENTATIONS OR WARRANTIES OF ANY KIND, EITHER EXPRESS OR IMPLIED, INCLUDING WARRANTIES OF TITLE, NONINFRINGEMENT, OR IMPLIED WARRANTIES OF MERCHANTABILITY OR FITNESS FOR A PARTICULAR PURPOSE. WITHOUT LIMITATION OF THE FOREGOING, LICENSEE AGREES THAT IT IS LICENSEE'S RESPONSIBILITY TO ENSURE, PRIOR TO USE OF ANY PLANS, THAT SUCH PLANS ARE ACCURATE, SUITABLE FOR LICENSEE'S PURPOSES AND THAT THEY COMPLY WITH ALL APPLICABLE LAWS.

3. IN NO EVENT SHALL Design with FRANK.INC OR ANY OF ITS DESIGNERS BE LIABLE FOR ANY INDIRECT, PUNITIVE, INCIDENTAL, SPECIAL, EXEMPLARY OR CONSEQUENTIAL DAMAGES ARISING OUT OF OR IN ANY WAY CONNECTED WITH THE USE OF OR INABILITY TO USE THE PLANS. Design with FRANK.INC 's LIABILITY FOR ANY DIRECT DAMAGES SHALL BE LIMITED TO (A) THE AMOUNT, IF ANY, LICENSEE PAID TO Design with FRANK.INC IN CONNECTION WITH THE MATTER GIVING RISE TO SUCH LIABILITY. SOME STATES OR JURISDICTIONS DO NOT ALLOW THE EXCLUSION OR LIMITATION OF LIABILITY FOR CONSEQUENTIAL OR INCIDENTAL DAMAGES AND THUS CERTAIN LIMITATIONS ABOVE MAY NOT APPLY TO LICENSEE. IF THIS LIMITATION OF LIABILITY OR THE EXCLUSION OF WARRANTY SET FORTH ABOVE IS HELD INAPPLICABLE OR UNENFORCEABLE FOR ANY REASON, Design with FRANK.INC 's MAXIMUM LIABILITY FOR ANY TYPE OF DAMAGES SHALL BE LIMITED TO $100.

4. No waiver of any obligation or right of either party will be effective unless in writing, executed by the party against whom it is being enforced. The terms of this License represent the entire agreement between Licensee and Design with FRANK.INC with respect to the subject matter hereof, and supersede any and all prior understandings, statements or representations, whether electronic, oral or written, regarding such subject matter. The terms of this License shall be deemed severable. In the event that a provision is determined to be unenforceable or invalid, it shall nonetheless be enforced to the fullest extent permitted by applicable laws, and such determination shall not affect the validity and enforceability of the remaining provisions.

5. This License Agreement is governed by the laws of the State of Delaware and United States Copyright Laws. The parties agree that any suit brought on any claim related to the provisions hereunder (including any suit for copyright infringement for exceeding the scope of the license) shall be brought exclusively in the state or federal courts located in Delaware.

Design with FRANK

Modern Cabin

THIS PLAN IS PROTECTED UNDER FEDRAL COPYRIGHT LAWS. ANY UNAUTHORIZED REPRODUCTION OR MODIFICATION OF THESE PLANS IS A VIOLATION OF COPYWRIGHT LAWS.

COPYRIGHT ALL RIGHTS RESERVED
DESIGN WITH FRANK.INC

Drawing Name

Legal

Drawing Scale

Layout ID

A.01.3

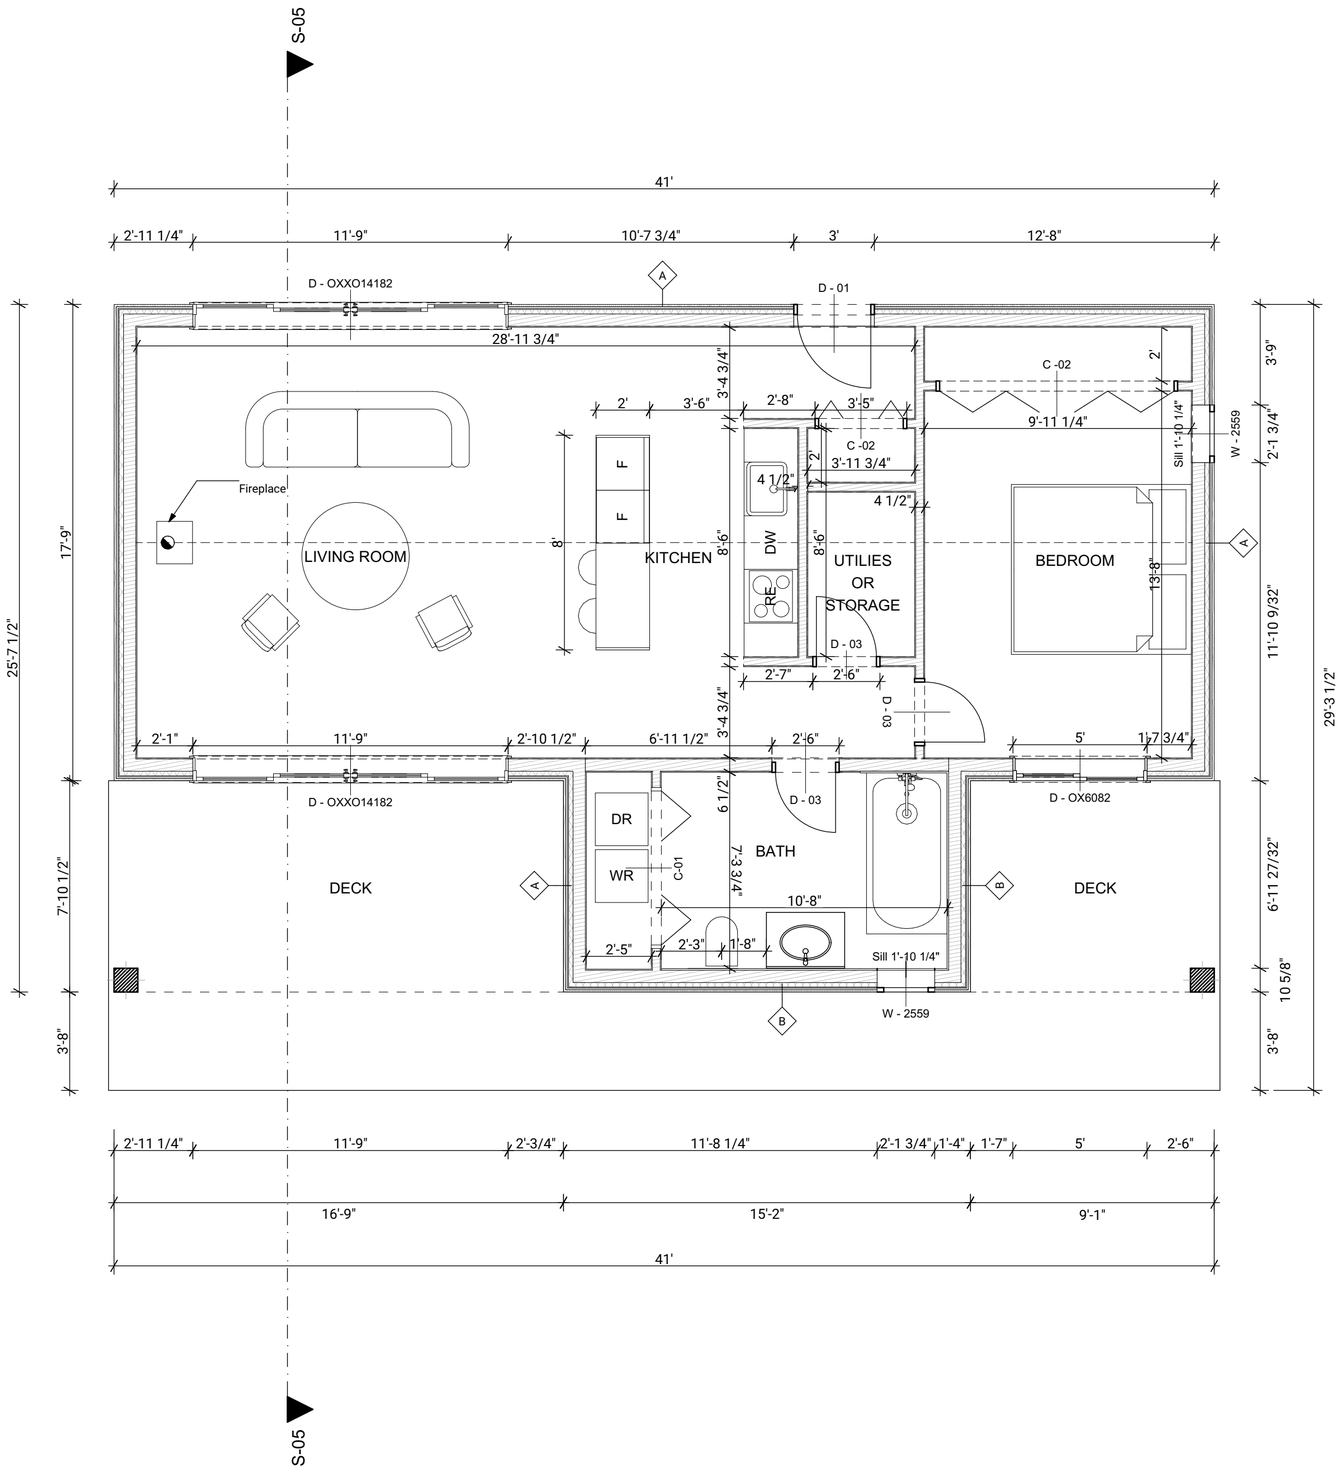

Design with FRANK

Modern Cabin

THIS PLAN IS PROTECTED UNDER FEDRAL COPYRIGHT LAWS. ANY UNAUTHORIZED REPRODUCTION OR MODIFICATION OF THESE PLANS IS A VIOLATION OF COPYWRIGHT LAWS.

COPYRIGHT ALL RIGHTS RESERVED
DESIGN WITH FRANK.INC

Drawing Name

Ground Plan

Drawing Scale

1/4" = 1'-0"

Layout ID

A.02.2

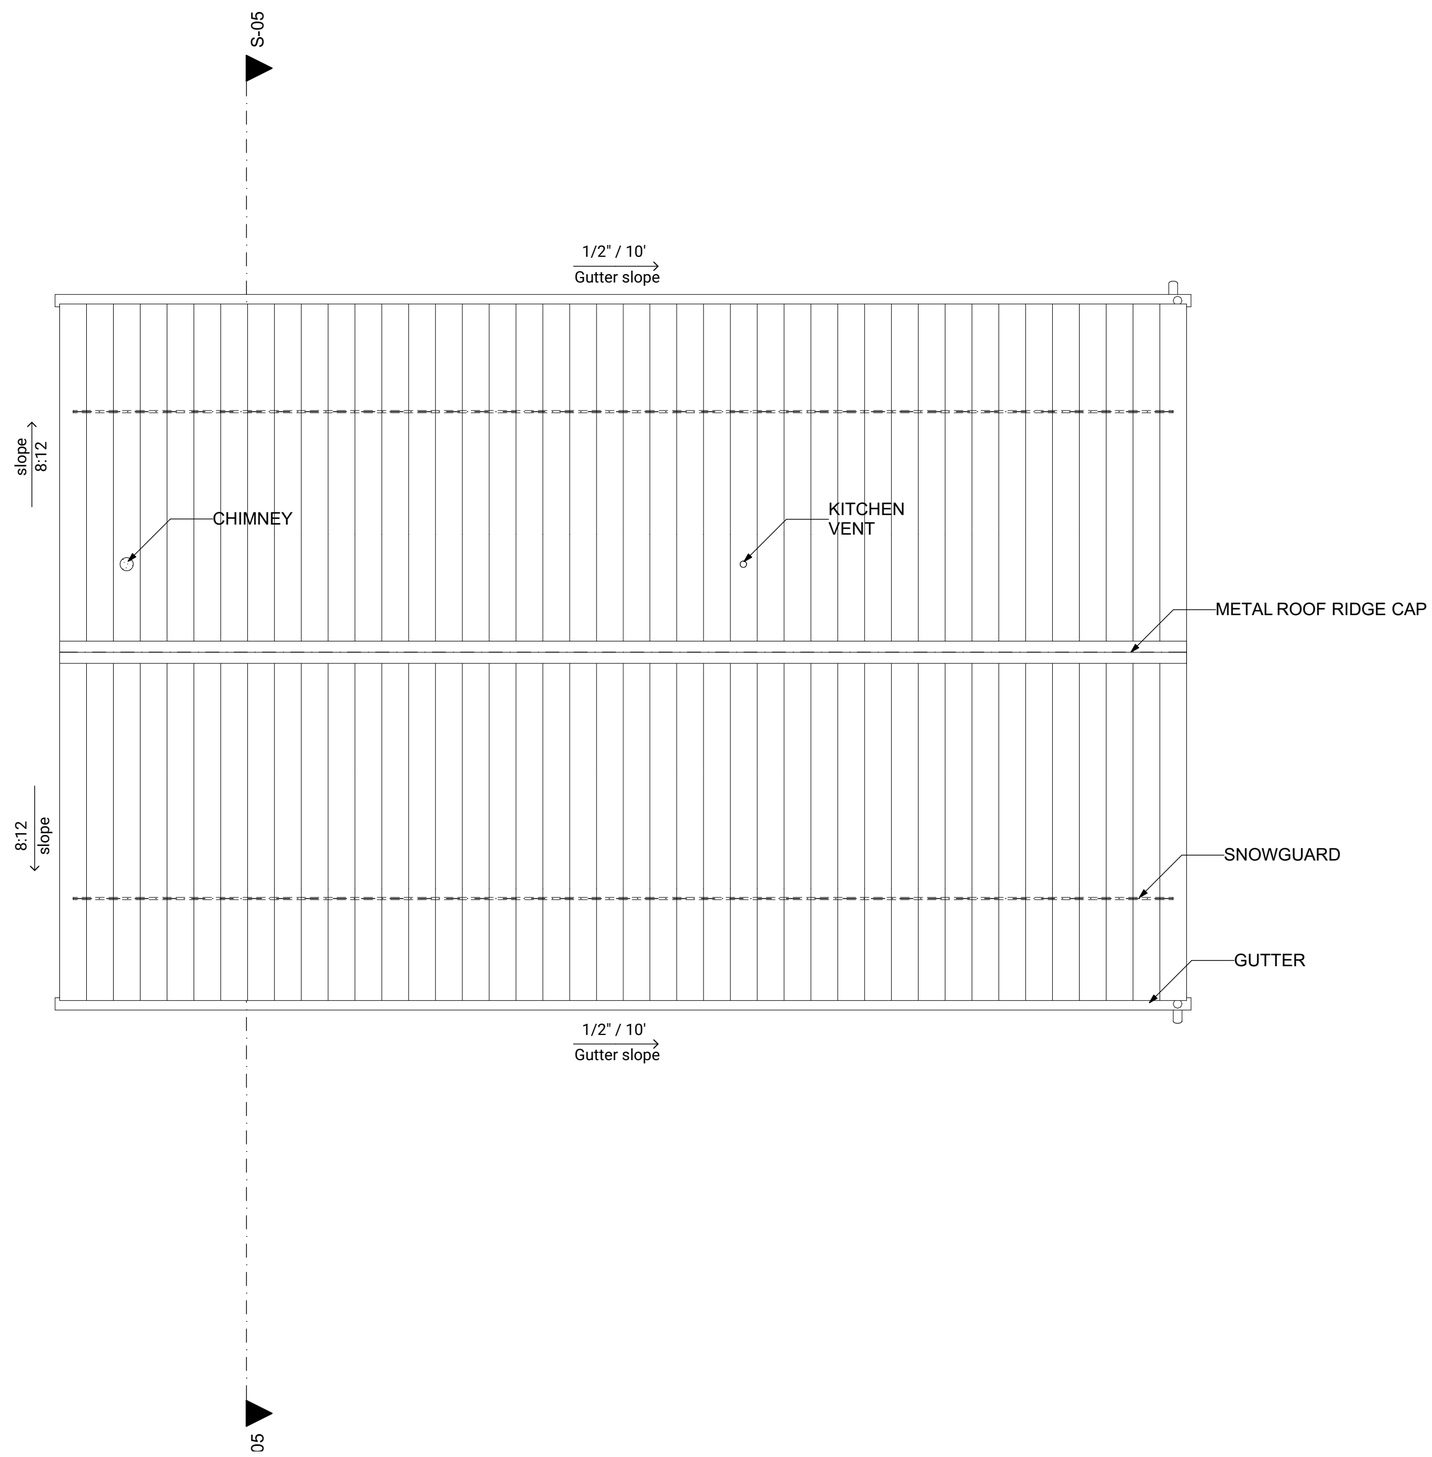

Design with FRANK

Modern Cabin

THIS PLAN IS PROTECTED UNDER FEDRAL COPYRIGHT LAWS. ANY UNAUTHORIZED REPRODUCTION OR MODIFICATION OF THESE PLANS IS A VIOLATION OF COPYWRIGHT LAWS.

COPYRIGHT ALL RIGHTS RESERVED
DESIGN WITH FRANK.INC

Drawing Name

Roof Plan

Drawing Scale

1/4" = 1'-0"

Layout ID

A.02.3

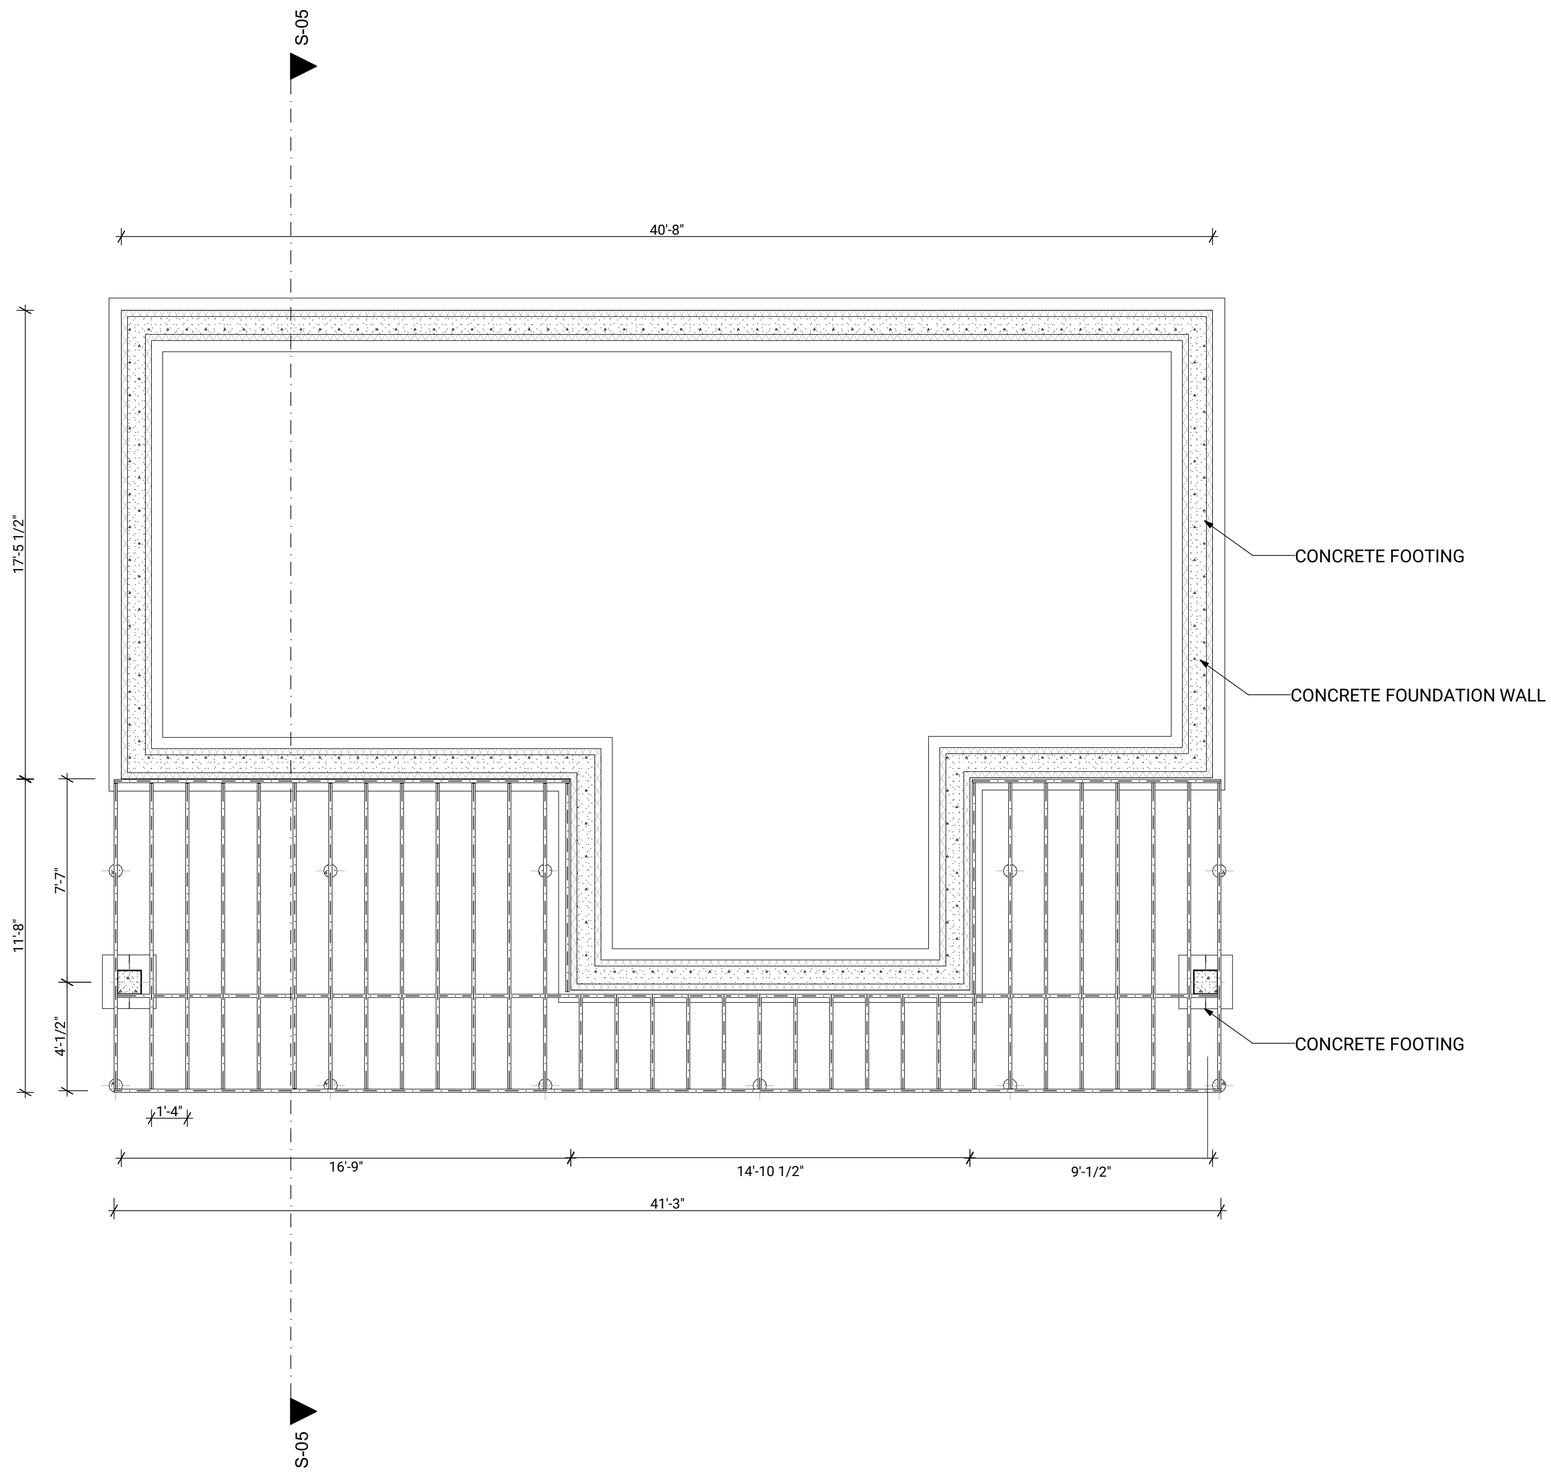

Design with FRANK

Modern Cabin

THIS PLAN IS PROTECTED UNDER FEDRAL COPYRIGHT LAWS. ANY UNAUTHORIZED REPRODUCTION OR MODIFICATION OF THESE PLANS IS A VIOLATION OF COPYWRIGHT LAWS.

COPYRIGHT ALL RIGHTS RESERVED
DESIGN WITH FRANK.INC

Drawing Name

Foundation Plan

Drawing Scale

1/4" = 1'-0"

Layout ID

A.02.1

Design with FRANK

Modern Cabin

THIS PLAN IS PROTECTED UNDER FEDRAL COPYRIGHT LAWS. ANY UNAUTHORIZED REPRODUCTION OR MODIFICATION OF THESE PLANS IS A VIOLATION OF COPYWRIGHT LAWS.

COPYRIGHT ALL RIGHTS RESERVED
DESIGN WITH FRANK.INC

Drawing Name

South Elevation

Drawing Scale

1/4" = 1'-0"

Layout ID

A.03.1

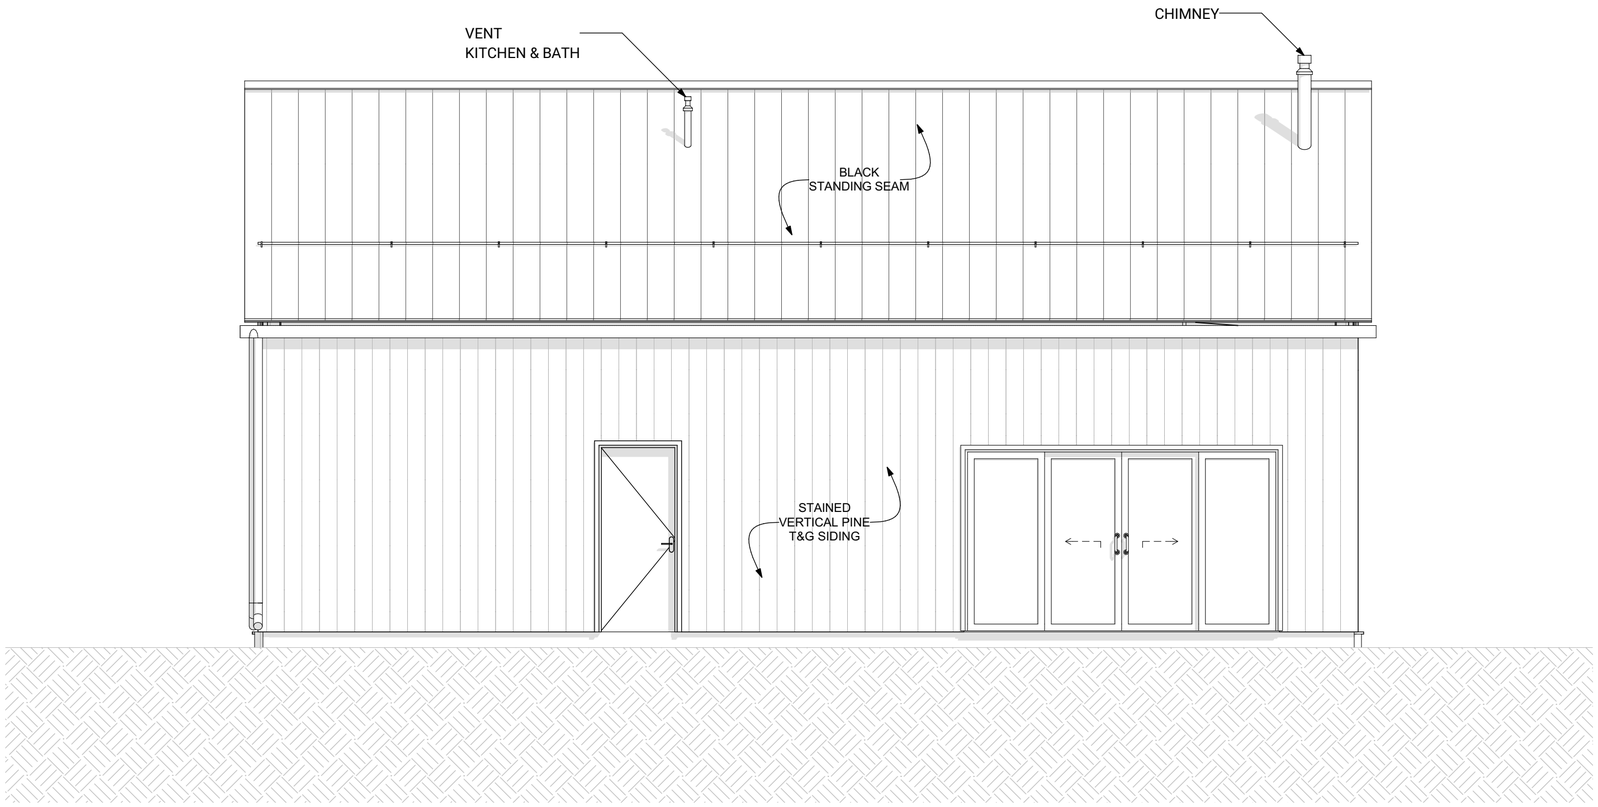

Design with FRANK

Modern Cabin

THIS PLAN IS PROTECTED UNDER FEDRAL COPYRIGHT LAWS. ANY UNAUTHORIZED REPRODUCTION OR MODIFICATION OF THESE PLANS IS A VIOLATION OF COPYWRIGHT LAWS.

COPYRIGHT ALL RIGHTS RESERVED
DESIGN WITH FRANK.INC

Drawing Name

North Elevation

Drawing Scale

1/4" = 1'-0"

Layout ID

A.03.2

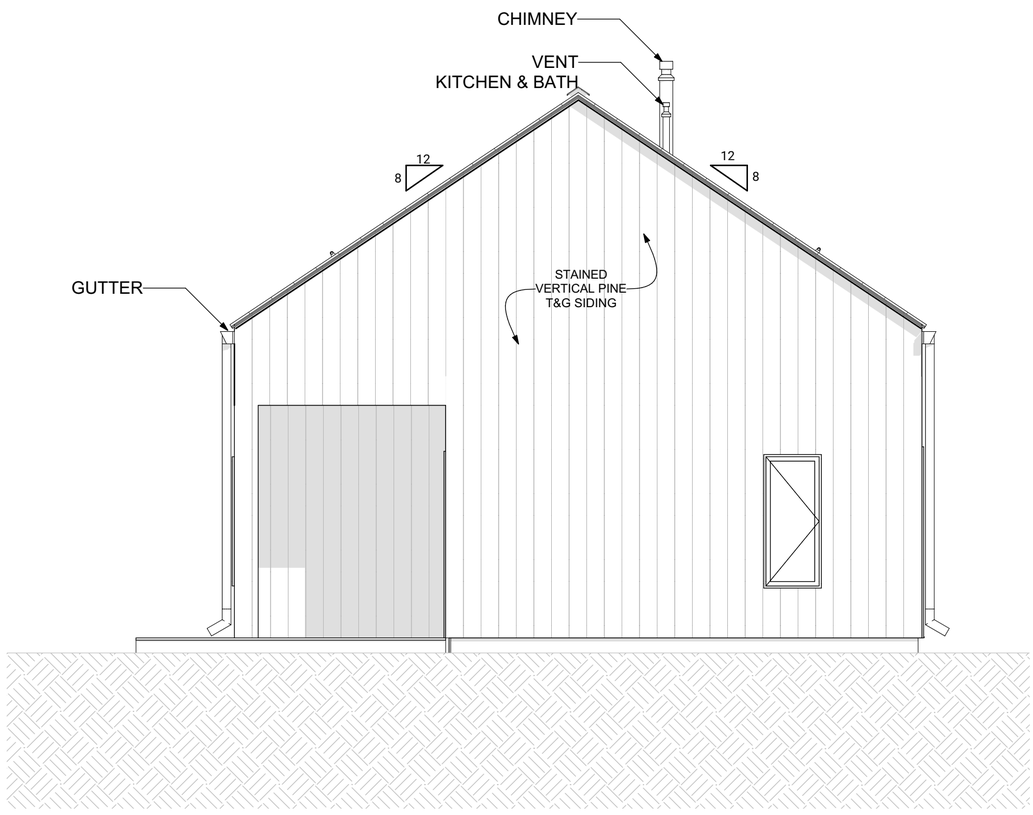

Design with FRANK

Modern Cabin

THIS PLAN IS PROTECTED UNDER FEDRAL COPYRIGHT LAWS. ANY UNAUTHORIZED REPRODUCTION OR MODIFICATION OF THESE PLANS IS A VIOLATION OF COPYWRIGHT LAWS.

COPYRIGHT ALL RIGHTS RESERVED
DESIGN WITH FRANK.INC

Drawing Name

East Elevation

Drawing Scale

1/4" = 1'-0"

Layout ID

A.03.3

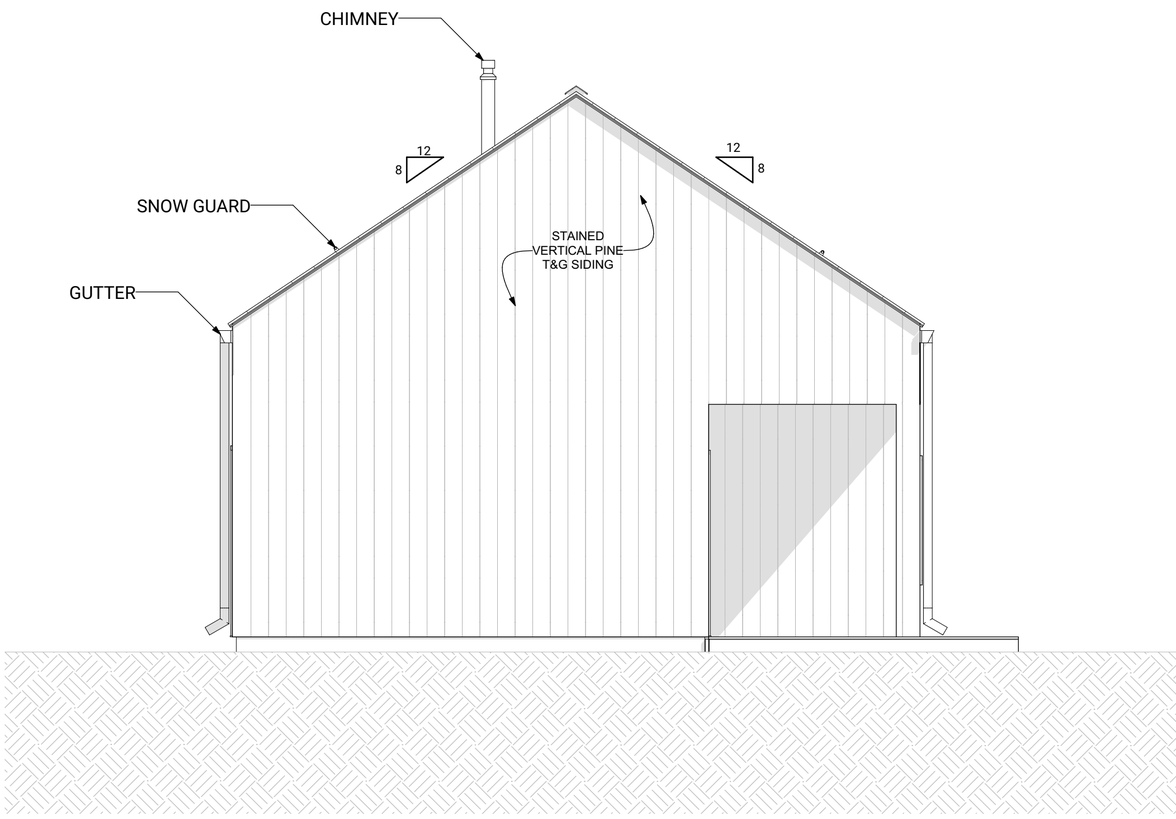

Design with FRANK

Modern Cabin

THIS PLAN IS PROTECTED UNDER FEDRAL COPYRIGHT LAWS. ANY UNAUTHORIZED REPRODUCTION OR MODIFICATION OF THESE PLANS IS A VIOLATION OF COPYWRIGHT LAWS.

COPYRIGHT ALL RIGHTS RESERVED
DESIGN WITH FRANK.INC

Drawing Name

West Elevation

Drawing Scale

1/4" = 1'-0"

Layout ID

A.03.4

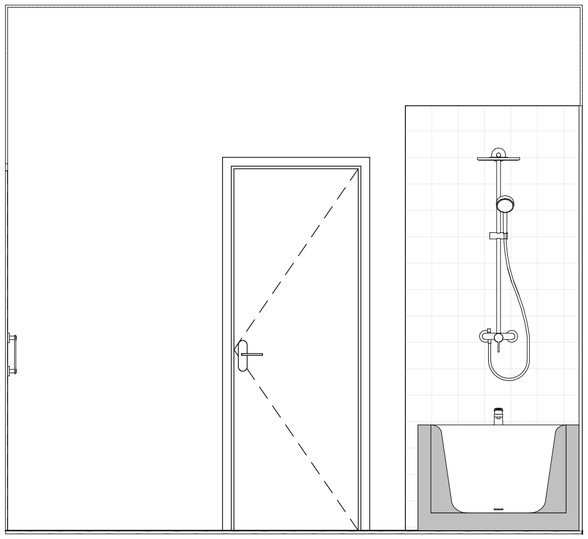

IE-01 01 Bathroom 1/2" = 1'-0"

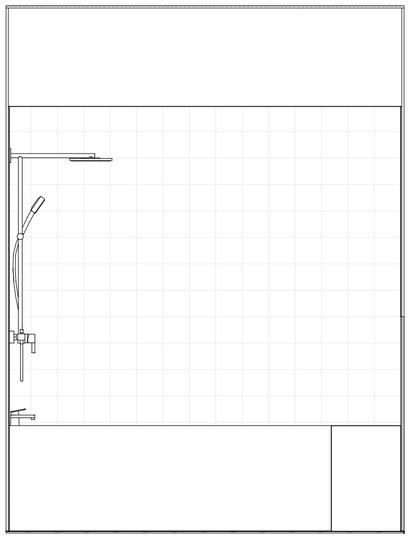

IE-01 02 Bathroom 1/2" = 1'-0"

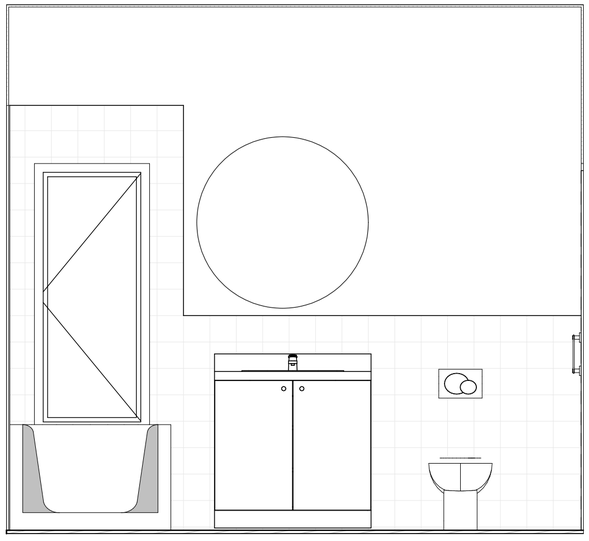

IE-01 03 Bathroom 1/2" = 1'-0"

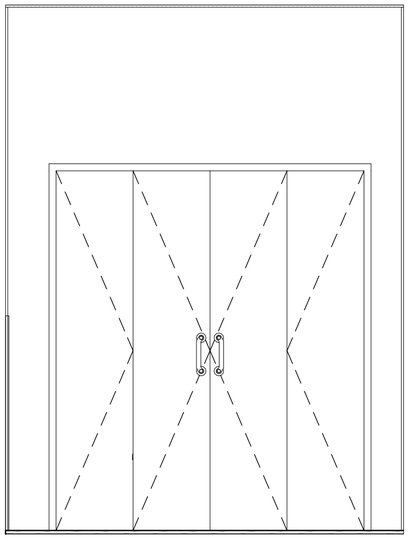

IE-01 04 Bathroom 1/2" = 1'-0"

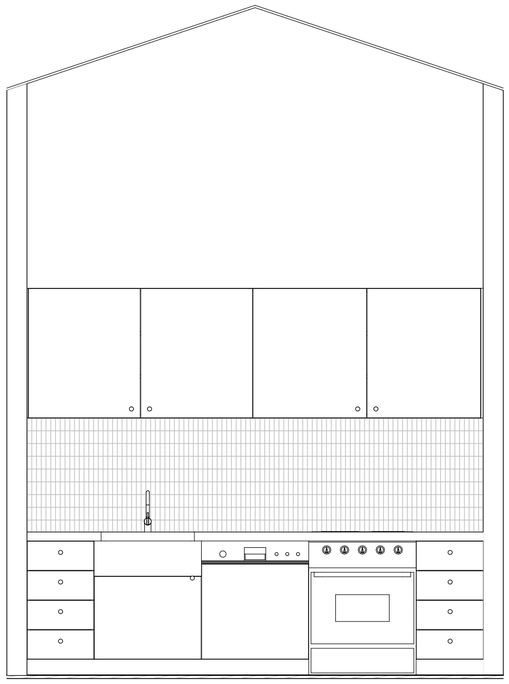

IE-05 01 Kitchen Elevation 1/2" = 1'-0"

Design with **FRANK**

Modern Cabin

THIS PLAN IS PROTECTED UNDER FEDRAL COPYRIGHT LAWS. ANY UNAUTHORIZED REPRODUCTION OR MODIFICATION OF THESE PLANS IS A VIOLATION OF COPYWRIGHT LAWS.

COPYRIGHT ALL RIGHTS RESERVED
DESIGN WITH FRANK.INC

Drawing Name

Bathroom & Kitchen Elevations

Drawing Scale

1/2" = 1'-0"

Layout ID

A.05.1

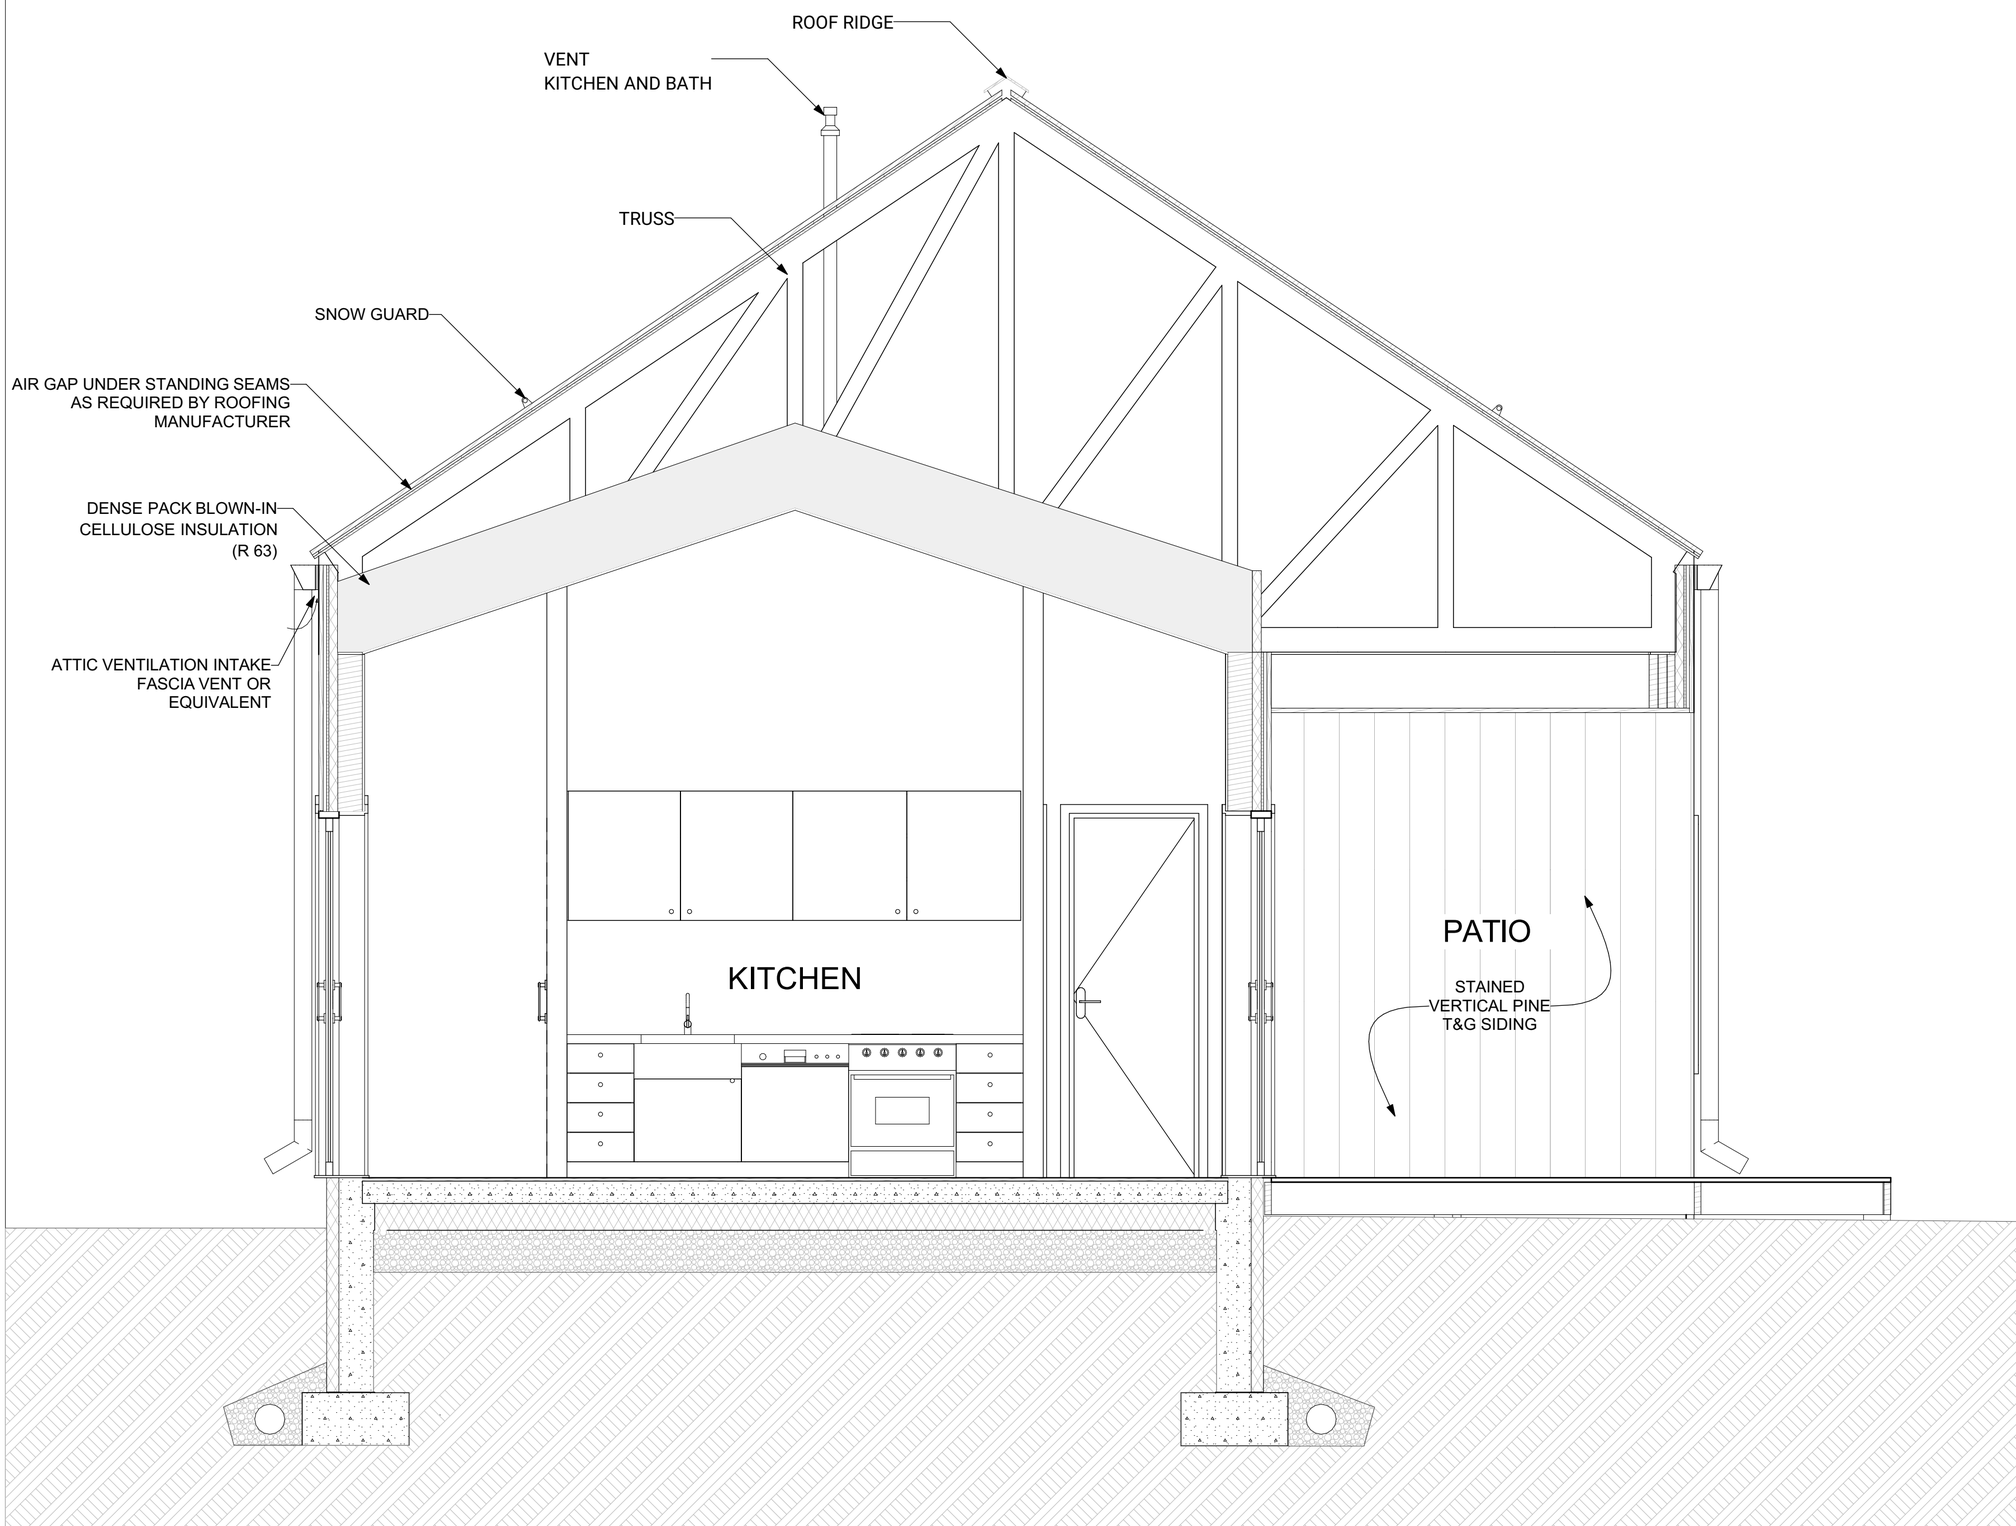

Design with FRANK

Modern Cabin

THIS PLAN IS PROTECTED UNDER FEDRAL COPYRIGHT LAWS. ANY UNAUTHORIZED REPRODUCTION OR MODIFICATION OF THESE PLANS IS A VIOLATION OF COPYWRIGHT LAWS.

COPYRIGHT ALL RIGHTS RESERVED
DESIGN WITH FRANK.INC

Drawing Name

S-01 Building Section

Drawing Scale

1/2" = 1'-0"

Layout ID

A.04.1

Exterior Doors List			
Element ID	D - 01	D - OX6082	D - OXXO14182
Quantity	1	1	2
W x H Size	3'×7'	5'×6'-10"	11'-9"×6'-10"
Sill height			
Head height	7'	6'-10"	6'-10"
2D Symbol	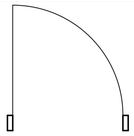	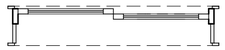	
3D Back View	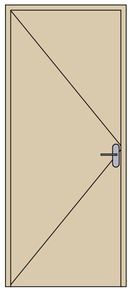	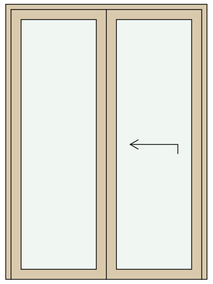	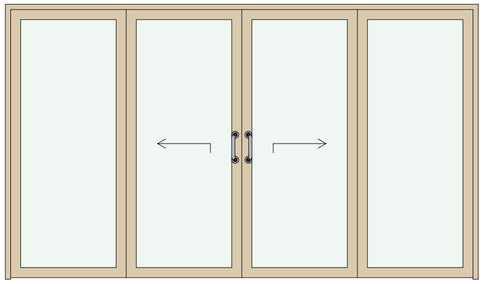
Series	ARCHITECT SERIES CONTEMPORARY®	ARCHITECT SERIES CONTEMPORARY®	ARCHITECT SERIES CONTEMPORARY®
Manufacturer	PELLA®	PELLA®	PELLA®

Interior Door	
Element ID	D - 03
Quantity	3
W x H Size	2'-6"×6'-10"
Sill height	
Head height	6'-10"
2D Symbol	
3D Front View	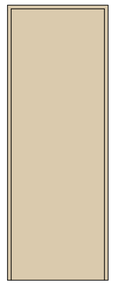

Window Schedule	
Element ID	W - 2559
Quantity	2
Nominal W x H Size	2'-1 3/4"×4'-11 3/4"
2D Symbol	
3D Back View	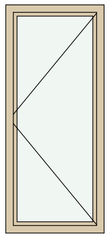
Series	ARCHITECT SERIES CONTEMPORARY®
Manufacturer	PELLA®

Design with FRANK

Modern Cabin

THIS PLAN IS PROTECTED UNDER FEDRAL COPYRIGHT LAWS. ANY UNAUTHORIZED REPRODUCTION OR MODIFICATION OF THESE PLANS IS A VIOLATION OF COPYWRIGHT LAWS.

COPYRIGHT ALL RIGHTS RESERVED
DESIGN WITH FRANK.INC

Drawing Name

Windows and Doors Lists

Drawing Scale

Layout ID

A.06

Object Inventory

Element ID	FU - 006	FU - 008	FU - 009	FU - 010	FU - 017	FU - 019	FU - 033
Object Name	Range Electric 23	Cabinet Base MultiD...	Cabinet Base Dishw...	Cabinet Belfast Sing...	Cabinet Wall Double...	Cabinet Base MultiD...	Refrigerator 23
Quantity	1	1	1	1	2	1	2
Length (A)	2'	1'-3"	2'	2'	4'-3"	1'-3"	1'-11 5/8"
Width (B)	2'	2'	2'	2'	11"	2'	1'-11 5/8"
Height (H)	2'-8"	2'-8"	2'-8"	2'-8"	2'-5"	2'-8"	2'-4"
2D Symbol	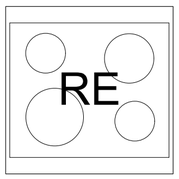			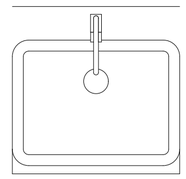			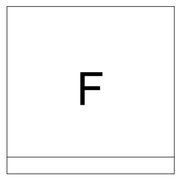
3D Front Axonometry			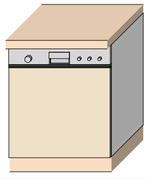	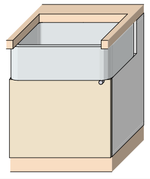	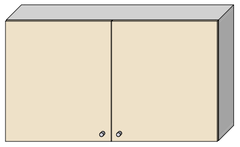		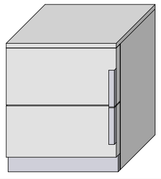

Design with FRANK

Modern Cabin

THIS PLAN IS PROTECTED UNDER FEDRAL COPYRIGHT LAWS. ANY UNAUTHORIZED REPRODUCTION OR MODIFICATION OF THESE PLANS IS A VIOLATION OF COPYWRIGHT LAWS.

COPYRIGHT ALL RIGHTS RESERVED
DESIGN WITH FRANK.INC

Drawing Name

Kitchen Cabinet

Drawing Scale

Layout ID

A.07