SHEET INDEX

A-000	COVER PAGE
A-001	GENERAL PLAN
A-002	ELEVATION
A-003	ELEVATION
B-101	FOUNDATION PLAN
B-102	GROUND FLOOR PLAN
B-103	SECOND FLOOR PLAN
B-104	DETAILED ELEVATION
B-105	DETAILED ELEVATION
B-106	ELECTRICAL PLAN
B-107	ROOF PLAN
B-108	ROOF FRAMING PLAN
B-109	SECTION DETAIL
B-110	STAIR DETAILS
C-101	DOOR SCHEDULE
C-102	WINDOW SCHEDULE

NOTES

1. DRAWINGS SHOULD BE PRINTED ON ANSI C SIZE PAPER TO ENSURE ACCURATE SCALE PRINTING
2. CONSTRUCTION DETAILS ILLUSTRATED IN THIS SET ARE TYPICAL, CONSULT WITH YOUR BUILDER FOR DETAILS THAT MEETS YOUR LOCAL BUILDING CODE.
3. MATERIALS AND FINISHES ILLUSTRATED IN THIS SET ARE TYPICAL, AND SHOULD BE VERIFIED BY YOUR BUILDER OR DESIGNER BEFORE CONSTRUCTION.
4. THIS DRAWING SET IS NOT INTENDED FOR PERMITTING OR CONSTRUCTION. CONSULT WITH YOUR LOCAL BUILDING DEPARTMENT FOR BUILDING CODE REQUIREMENTS.

AXONOMETRIC VIEW

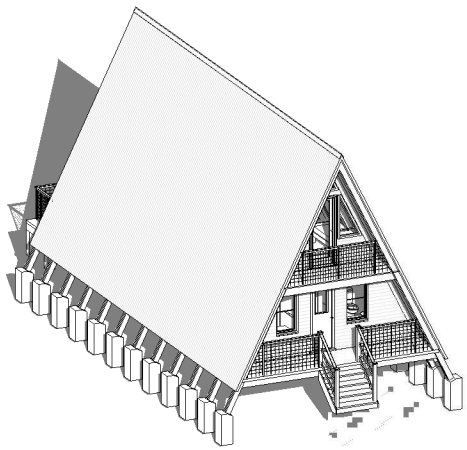

SYMBOLS LEGEND

- SECTION MARKER
- ELEVATION MARKER
- INTERIOR ELEVATIONS
- DETAIL CALLOUT
- DATUM MARKER
- SLOPE MARKER
- COMPASS (TRUE NORTH)
- WINDOW CALLOUT
- DOOR CALLOUT
- SOIL
- CONCRETE
- BRICK
- CMU BLOCK
- RIGID INSULATION
- BATT INSULATION
- DIMENSIONAL LUMBER
- ELECTRIC OUTLET
- SWITCH
- CEILING LIGHT
- RECESSED LIGHT
- WALL-MOUNTED LIGHT
- CEILING FAN

LICENSE & DISCLAIMER

1. THE WORK INCLUDED WITHIN THESE DRAWINGS DOES NOT REPRESENT A LEGAL CONTRACT; NOR DOES IT CONSTITUTE ARCHITECTURAL SERVICES. NO PERSON OR ORGANIZATION MAKES ANY WARRANTY, EXPRESS OR IMPLIED, REGARDING THE INFORMATION PROVIDED. THE CRATORS DISCLAIM LIABILITY FOR ANY DAMAGES THAT MAY RESULT FROM THE USE OF THESE DRAWINGS.

2. THIS PLAN HAS BEEN PREPARED TO MEET PROFESSIONAL STANDARDS AND PRACTICES. HOWEVER, BUILDING CODE REQUIREMENTS VERY WITH LOCATION AND CHANGE FROM TIME TO TIME. BEFORE STARTING CONSTRUCTION THE CONTRACTOR MUST REVIEW AND BE RESPONSIBLE FOR ALL DIMENSIONS AND OTHER DETAILS AND SHOULD REVIEW PLANS TO INSURE THEY MEET CURRENT REQUIREMENTS. THE CONTRACTOR ASSUMES FULL RESPONSIBILITY TO VERIFY THE CONDITIONS, DIMENSIONS, AND STRUCTURAL DETAILS OF THE BUILDING, AND ASSUMES FULL LIABILITY FOR ANY PROBLEMS THAT MAY ARISE DUE TO POSSIBLE ERRORS ON THESE PLANS. ALL FEDERAL, STATE AND LOCAL CODES. ORDINANCES, REGULATIONS, ETC.,SHALL BE CONSIDERED AS PART OF SPECIFICATIONS FOR THIS BUILDING AND SHALL TAKE PRECEDENCE OVER ANYTHING SHOWN, DESCRIBED OR IMPLIED WHERE SAME ARE AT VARIANCE. USE OF THESE PLANS CONSTITUTES COMPLIANCE WITH THE ABOVE TERMS.

3. THESE PLANS ARE OWNED AND COPYRIGHTED BY DIYWEEKEND AND ARE INTENTED FOR PERSONAL USE ONLY. COPYING OR DISTRIBUTING WITHOUT PERMISSION IS ILLEGAL AND CAN RESULT UP TO FINES OF $100,000 BY COURT. THESE PLANS ARE NOT INTENDED FOR COMMERCIAL USE, AND CANNOT BE DISTRIBUTED FOR CAPITAL GAINS.

No.	Description	Date

22x36 A-FRAME CABIN

COVER PAGE

Project number	DC-003
Date	
Drawn by	T.H
Checked by	E.S

A-000

Sheet Number	
Scale	

Copyrighted @DIYWEEKEND

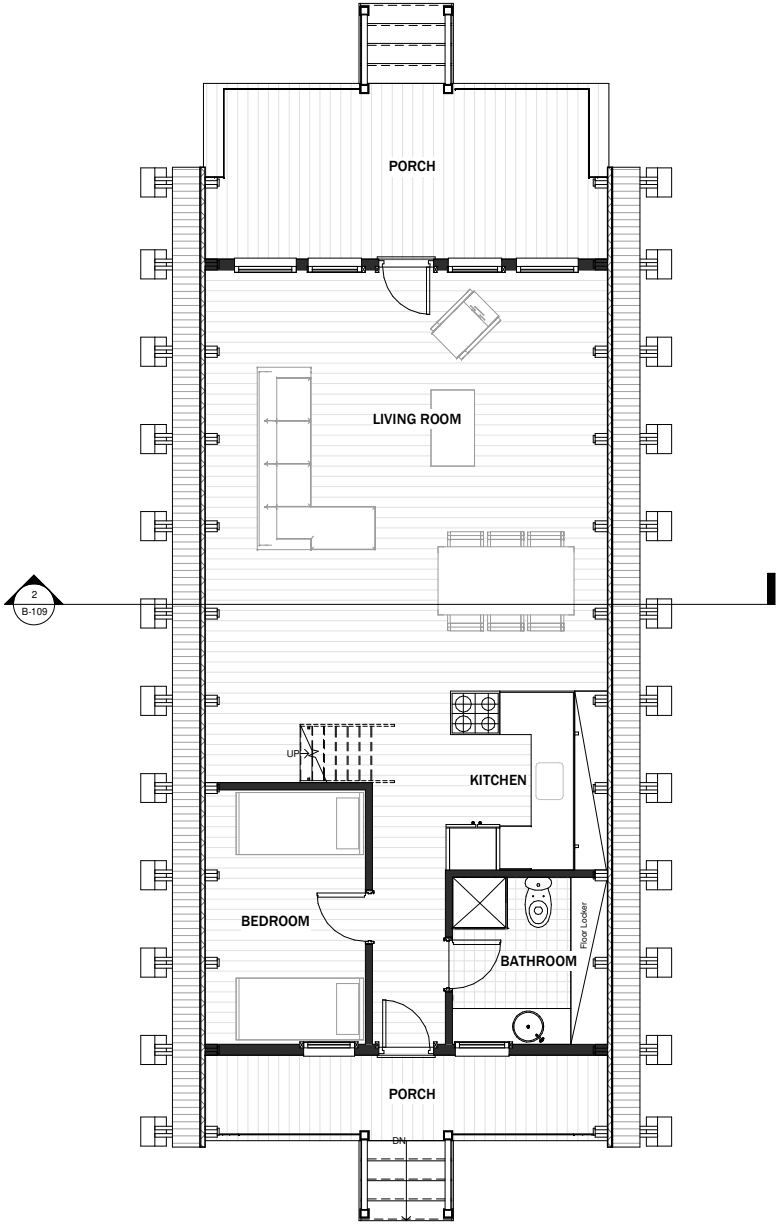

N

GROUND FLOOR PLAN

SCALE = 1/4" : 1' - 0"

NOTES

1. DRAWINGS SHOULD BE PRINTED ON ANSI C SIZE PAPER TO ENSURE ACCURATE SCALE PRINTING 1/4" = 1'-0"
2. CONSTRUCTION DETAILS ILLUSTRATED IN THIS SET ARE TYPICAL, CONSULT WITH YOUR BUILDER FOR DETAILS THAT MEETS YOUR LOCAL BUILDING CODE.
3. MATERIALS AND FINISHES ILLUSTRATED IN THIS SET ARE TYPICAL, AND SHOULD BE VERIFIED BY YOUR BUILDER OR DESIGNER BEFORE CONSTRUCTION.
4. THIS DRAWING SET IS NOT INTENDED FOR PERMITTING OR CONSTRUCTION. CONSULT WITH YOUR LOCAL BUILDING DEPARTMENT FOR BUILDING CODE REQUIREMENTS.

No.	Description	Date

22x36 A-FRAME CABIN

GROUND FLOOR PLAN

Project number	DC-003
Date	
Drawn by	T.H
Checked by	E.S
A-001	
Sheet Number	
Scale	1/4" = 1'-0"

Copyrighted @DIYWEEKEND

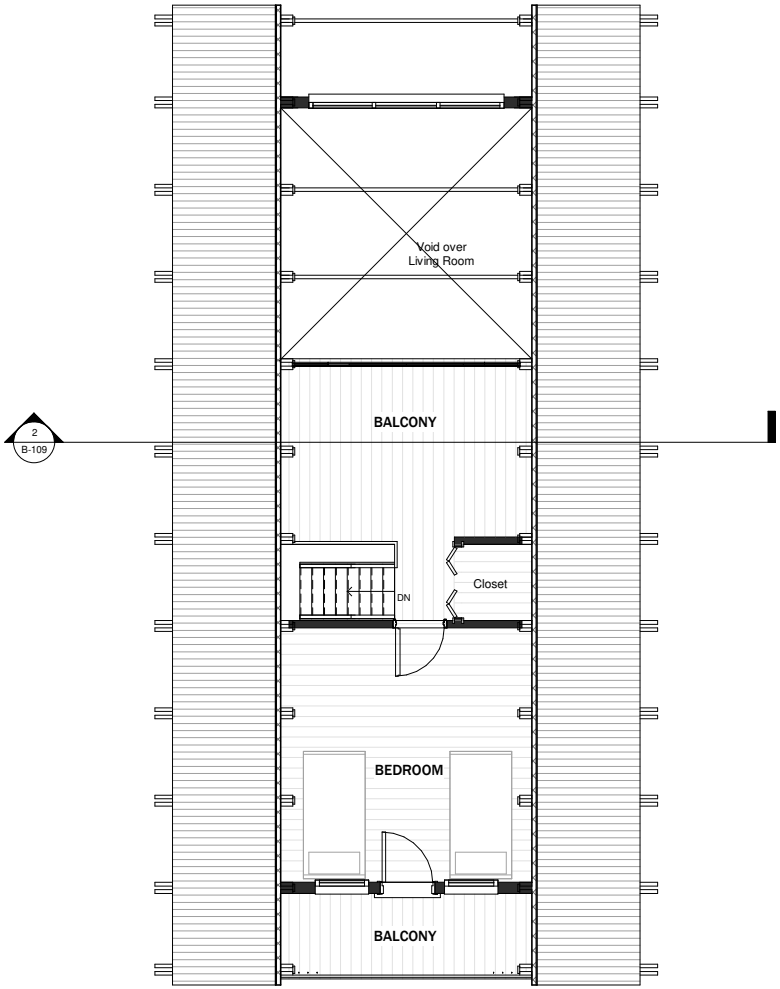

SECOND FLOOR PLAN

SCALE = 1/4" : 1' - 0"

NOTES

1. DRAWINGS SHOULD BE PRINTED ON ANSI C SIZE PAPER TO ENSURE ACCURATE SCALE PRINTING 1/4" = 1'-0"
2. CONSTRUCTION DETAILS ILLUSTRATED IN THIS SET ARE TYPICAL, CONSULT WITH YOUR BUILDER FOR DETAILS THAT MEETS YOUR LOCAL BUILDING CODE.
3. MATERIALS AND FINISHES ILLUSTRATED IN THIS SET ARE TYPICAL, AND SHOULD BE VERIFIED BY YOUR BUILDER OR DESIGNER BEFORE CONSTRUCTION.
4. THIS DRAWING SET IS NOT INTENDED FOR PERMITTING OR CONSTRUCTION. CONSULT WITH YOUR LOCAL BUILDING DEPARTMENT FOR BUILDING CODE REQUIREMENTS.

No.	Description	Date

22x36 A-FRAME CABIN

SECOND FLOOR PLAN

Project number	**DC-003**
Date	
Drawn by	T.H
Checked by	E.S

A-002

Sheet Number	
Scale	**1/4" = 1'-0"**

Copyrighted @DIYWEEKEND

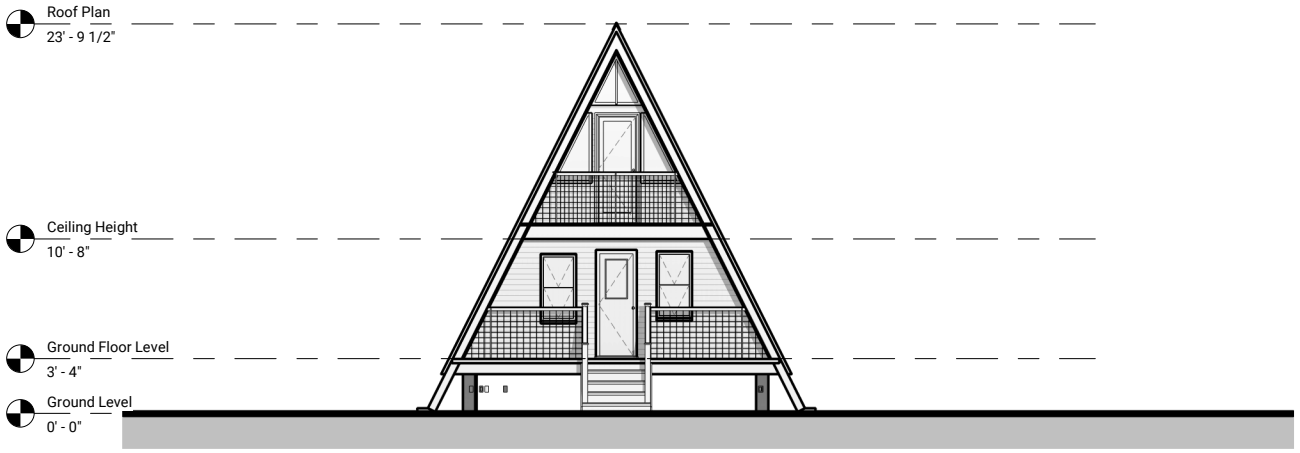

SOUTH EXTERIOR ELEVATION

SCALE = 1/4" : 1' - 0"

NORTH EXTERIOR ELEVATION

SCALE = 1/4" : 1' - 0"

NOTES

1. DRAWINGS SHOULD BE PRINTED ON ANSI C SIZE PAPER TO ENSURE ACCURATE SCALE PRINTING 3/16" = 1'-0"
2. CONSTRUCTION DETAILS ILLUSTRATED IN THIS SET ARE TYPICAL, CONSULT WITH YOUR BUILDER FOR DETAILS THAT MEETS YOUR LOCAL BUILDING CODE.
3. MATERIALS AND FINISHES ILLUSTRATED IN THIS SET ARE TYPICAL, AND SHOULD BE VERIFIED BY YOUR BUILDER OR DESIGNER BEFORE CONSTRUCTION.
4. THIS DRAWING SET IS NOT INTENDED FOR PERMITTING OR CONSTRUCTION. CONSULT WITH YOUR LOCAL BUILDING DEPARTMENT FOR BUILDING CODE REQUIREMENTS.

No.	Description	Date

22x36 A-FRAME CABIN

ELEVATION I

Project number	**DC-003**
Date	
Drawn by	T.H
Checked by	E.S

A-003

Sheet Number	
Scale	**3/16" = 1'-0"**

Copyrighted @DIYWEEKEND

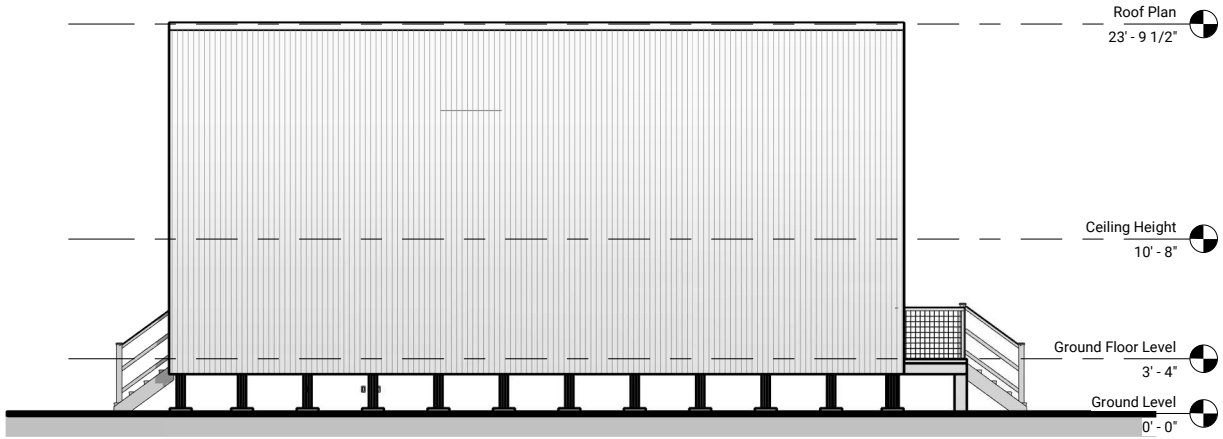

EAST EXTERIOR ELEVATION

SCALE = 3/16" : 1' - 0"

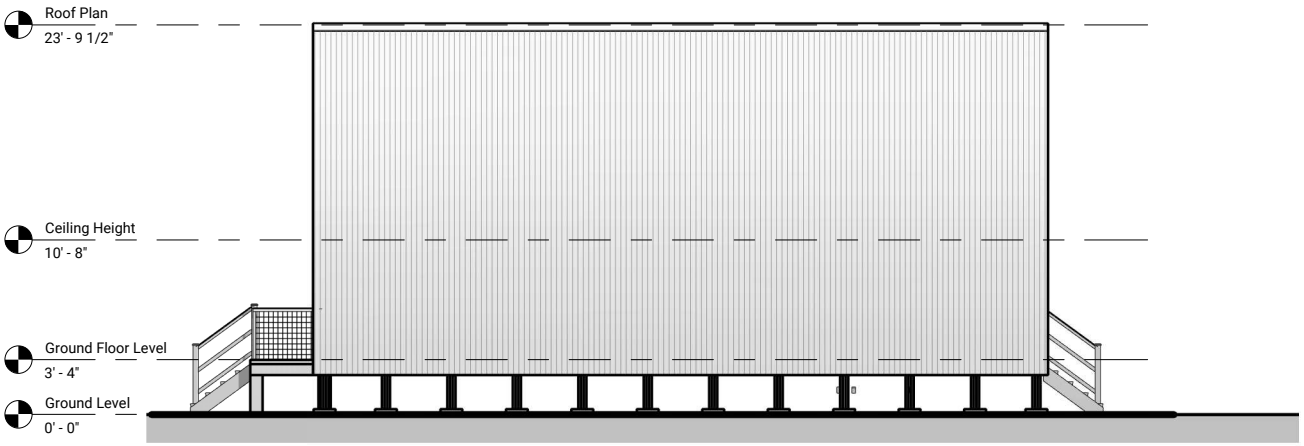

WEST EXTERIOR ELEVATION

SCALE = 3/16" : 1' - 0"

NOTES

1. DRAWINGS SHOULD BE PRINTED ON ANSI C SIZE PAPER TO ENSURE ACCURATE SCALE PRINTING 3/16" = 1'-0"
2. CONSTRUCTION DETAILS ILLUSTRATED IN THIS SET ARE TYPICAL, CONSULT WITH YOUR BUILDER FOR DETAILS THAT MEETS YOUR LOCAL BUILDING CODE.
3. MATERIALS AND FINISHES ILLUSTRATED IN THIS SET ARE TYPICAL, AND SHOULD BE VERIFIED BY YOUR BUILDER OR DESIGNER BEFORE CONSTRUCTION.
4. THIS DRAWING SET IS NOT INTENDED FOR PERMITTING OR CONSTRUCTION. CONSULT WITH YOUR LOCAL BUILDING DEPARTMENT FOR BUILDING CODE REQUIREMENTS.

No.	Description	Date

22x36 A-FRAME CABIN

ELEVATIONS II

Project number	DC-003
Date	
Drawn by	T.H
Checked by	E.S

A-004

Sheet Number	
Scale	3/16" = 1'-0"

Copyrighted @DIYWEEKEND

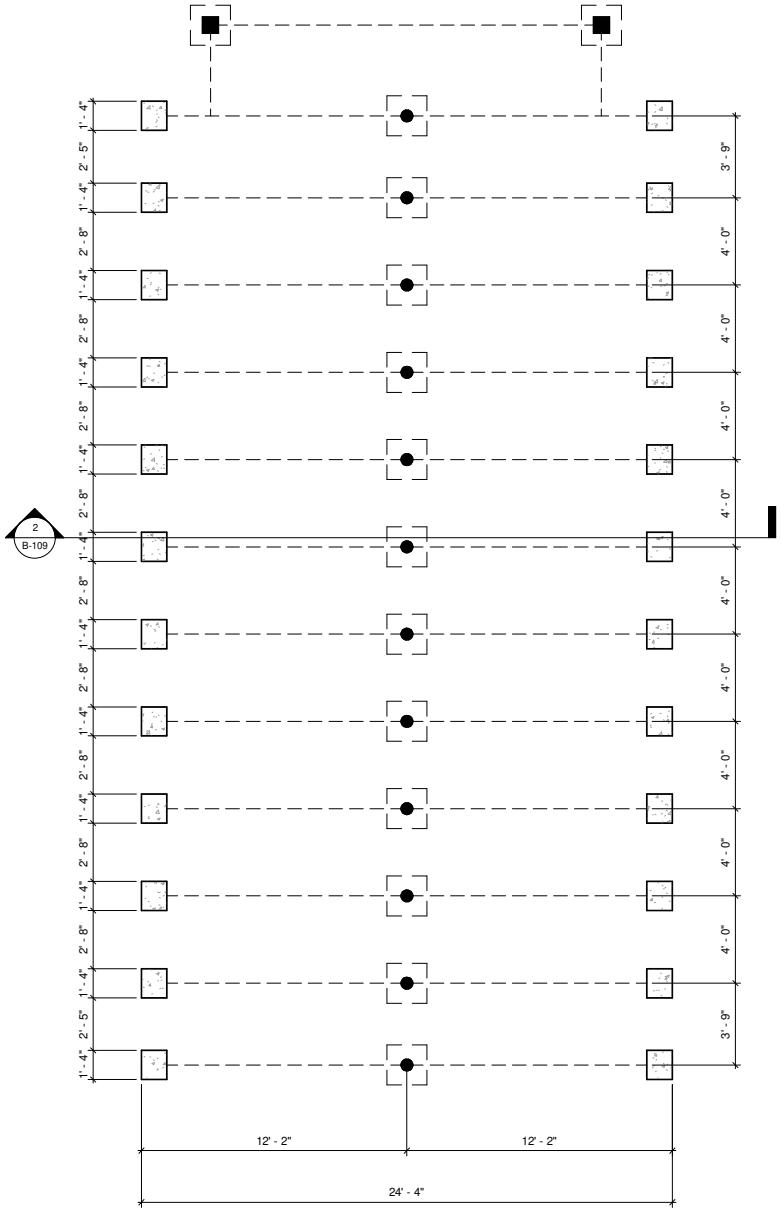

FOUNDATION PLAN

SCALE = 1/4" : 1' - 0"

NOTES

1. DRAWINGS SHOULD BE PRINTED ON ANSI C SIZE PAPER TO ENSURE ACCURATE SCALE PRINTING 1/4" = 1'-0"
2. CONSTRUCTION DETAILS ILLUSTRATED IN THIS SET ARE TYPICAL, CONSULT WITH YOUR BUILDER FOR DETAILS THAT MEETS YOUR LOCAL BUILDING CODE.
3. MATERIALS AND FINISHES ILLUSTRATED IN THIS SET ARE TYPICAL, AND SHOULD BE VERIFIED BY YOUR BUILDER OR DESIGNER BEFORE CONSTRUCTION.
4. THIS DRAWING SET IS NOT INTENDED FOR PERMITTING OR CONSTRUCTION. CONSULT WITH YOUR LOCAL BUILDING DEPARTMENT FOR BUILDING CODE REQUIREMENTS.

No.	Description	Date

22x36 A-FRAME CABIN

FOUNDATION PLAN

Project number	**DC-003**
Date	
Drawn by	T.H
Checked by	E.S

B-101

Sheet Number	
Scale	**1/4" = 1'-0"**

Copyrighted @DIYWEEKEND

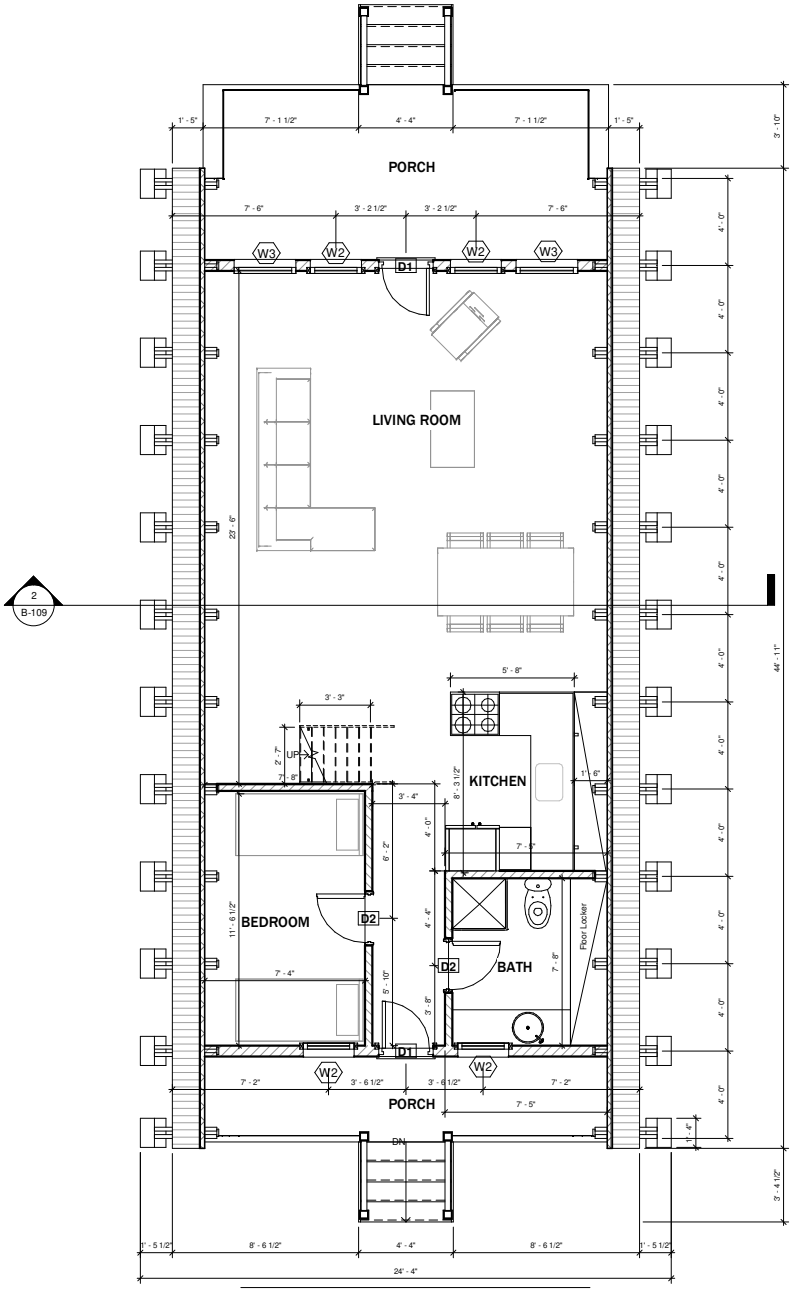

GROUND FLOOR PLAN

SCALE = 1/4" : 1' - 0"

N

NOTES

1. DRAWINGS SHOULD BE PRINTED ON ANSI C SIZE PAPER TO ENSURE ACCURATE SCALE PRINTING 1/4" = 1'-0"
2. CONSTRUCTION DETAILS ILLUSTRATED IN THIS SET ARE TYPICAL, CONSULT WITH YOUR BUILDER FOR DETAILS THAT MEETS YOUR LOCAL BUILDING CODE.
3. MATERIALS AND FINISHES ILLUSTRATED IN THIS SET ARE TYPICAL, AND SHOULD BE VERIFIED BY YOUR BUILDER OR DESIGNER BEFORE CONSTRUCTION.
4. THIS DRAWING SET IS NOT INTENDED FOR PERMITTING OR CONSTRUCTION. CONSULT WITH YOUR LOCAL BUILDING DEPARTMENT FOR BUILDING CODE REQUIREMENTS.

No.	Description	Date

22x36 A-FRAME CABIN

GROUND FLOOR

Project number	**DC-003**
Date	
Drawn by	T.H
Checked by	E.S

B-102

Sheet Number	
Scale	**1/4" = 1'-0"**

Copyrighted @DIYWEEKEND

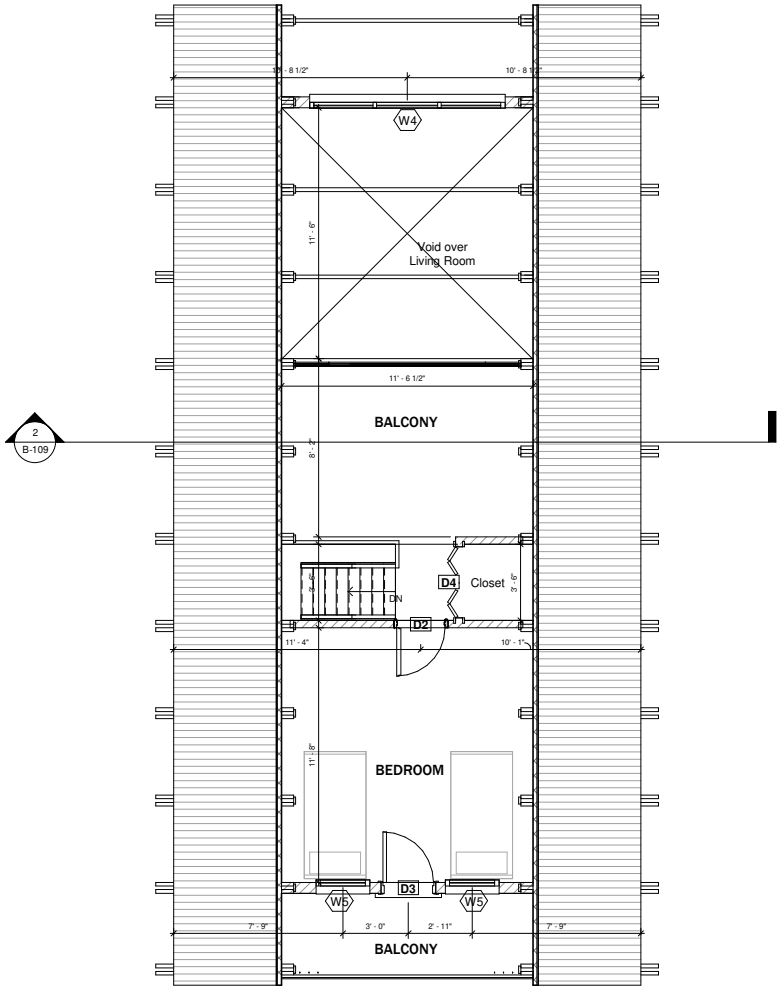

SECOND FLOOR PLAN

SCALE = 1/4" : 1' - 0"

NOTES

1. DRAWINGS SHOULD BE PRINTED ON ANSI C SIZE PAPER TO ENSURE ACCURATE SCALE PRINTING 1/4" = 1'-0"
2. CONSTRUCTION DETAILS ILLUSTRATED IN THIS SET ARE TYPICAL, CONSULT WITH YOUR BUILDER FOR DETAILS THAT MEETS YOUR LOCAL BUILDING CODE.
3. MATERIALS AND FINISHES ILLUSTRATED IN THIS SET ARE TYPICAL, AND SHOULD BE VERIFIED BY YOUR BUILDER OR DESIGNER BEFORE CONSTRUCTION.
4. THIS DRAWING SET IS NOT INTENDED FOR PERMITTING OR CONSTRUCTION. CONSULT WITH YOUR LOCAL BUILDING DEPARTMENT FOR BUILDING CODE REQUIREMENTS.

No.	Description	Date

22x36 A-FRAME CABIN

SECOND FLOOR PLAN

Project number	**DC-003**
Date	
Drawn by	T.H
Checked by	E.S

B-103

Sheet Number	
Scale	**1/4" = 1'-0"**

Copyrighted @DIYWEEKEND

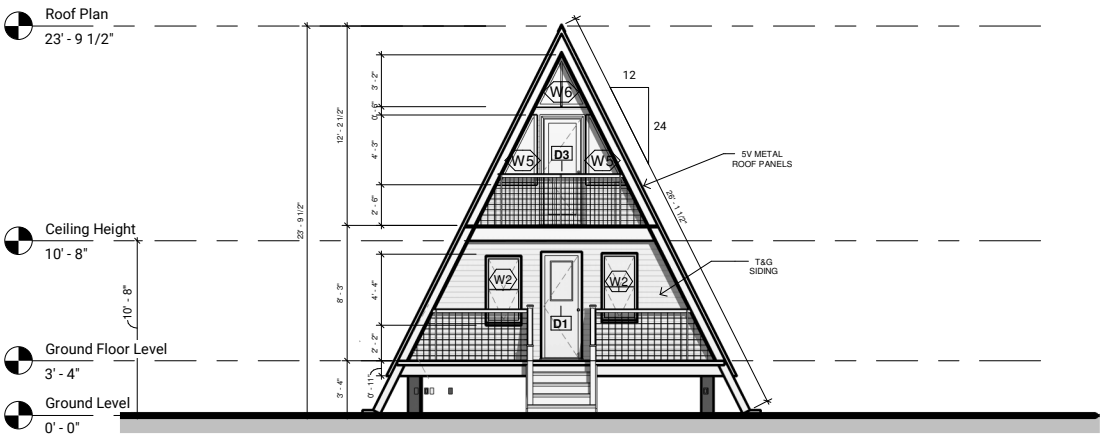

SOUTH EXTERIOR ELEVATION

SCALE = 1/4" : 1' - 0"

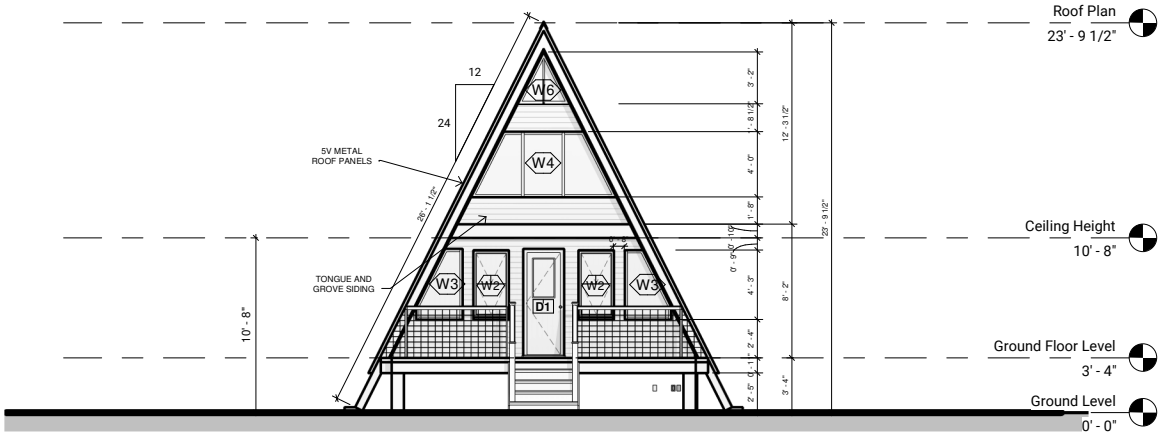

NORTH EXTERIOR ELEVATION

SCALE = 1/4" : 1' - 0"

NOTES

1. DRAWINGS SHOULD BE PRINTED ON ANSI C SIZE PAPER TO ENSURE ACCURATE SCALE PRINTING 3/16" = 1'-0"
2. CONSTRUCTION DETAILS ILLUSTRATED IN THIS SET ARE TYPICAL, CONSULT WITH YOUR BUILDER FOR DETAILS THAT MEETS YOUR LOCAL BUILDING CODE.
3. MATERIALS AND FINISHES ILLUSTRATED IN THIS SET ARE TYPICAL, AND SHOULD BE VERIFIED BY YOUR BUILDER OR DESIGNER BEFORE CONSTRUCTION.
4. THIS DRAWING SET IS NOT INTENDED FOR PERMITTING OR CONSTRUCTION. CONSULT WITH YOUR LOCAL BUILDING DEPARTMENT FOR BUILDING CODE REQUIREMENTS.

No.	Description	Date

22x36 A-FRAME CABIN

NORTH & SOUTH ELEVATION

Project number	DC-003
Date	
Drawn by	T.H
Checked by	E.S

B-104

Sheet Number	
Scale	3/16" = 1'-0"

Copyrighted @DIYWEEKEND

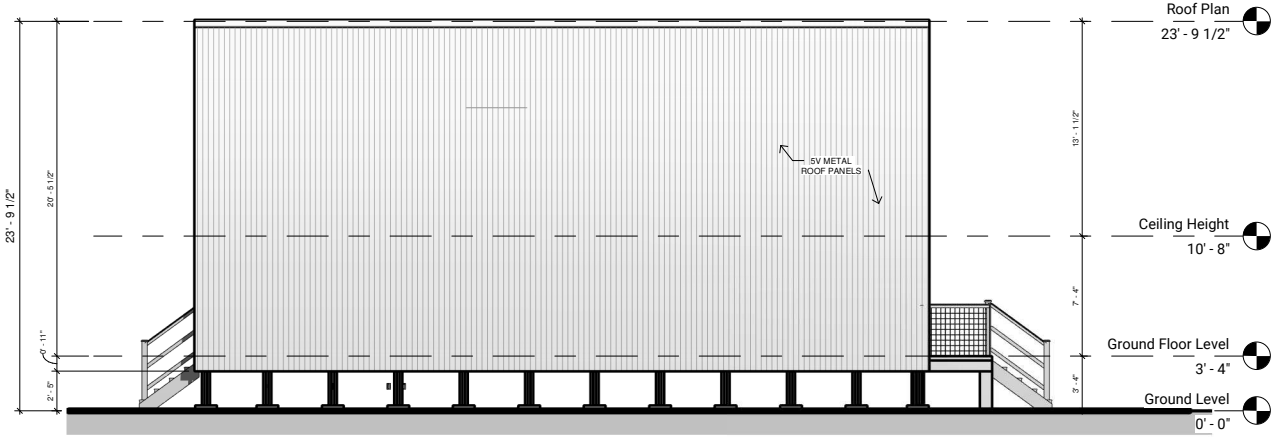

EAST EXTERIOR ELEVATION

SCALE = 3/16" : 1' - 0"

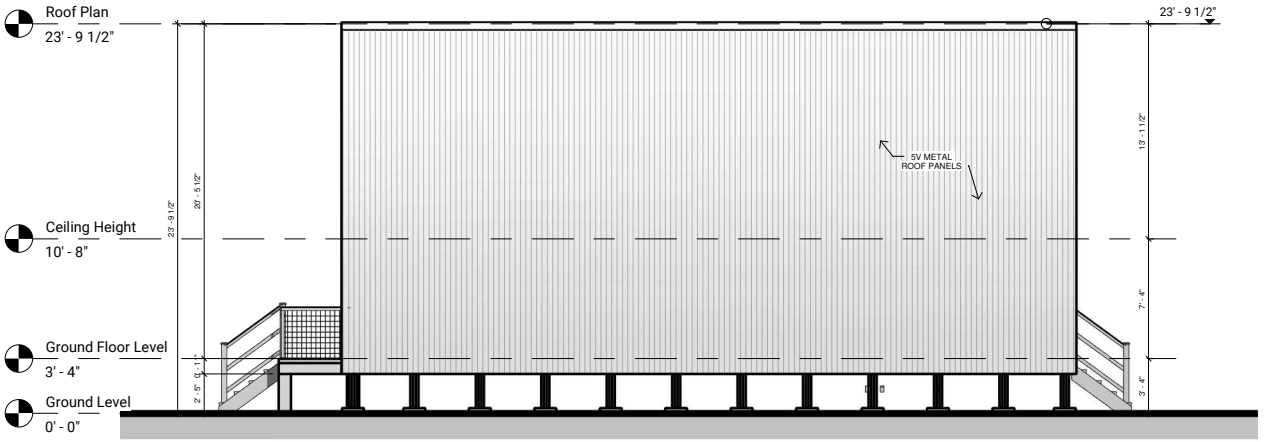

WEST EXTERIOR ELEVATION

SCALE = 3/16" : 1' - 0"

NOTES

1. DRAWINGS SHOULD BE PRINTED ON ANSI C SIZE PAPER TO ENSURE ACCURATE SCALE PRINTING 3/16" = 1'-0"
2. CONSTRUCTION DETAILS ILLUSTRATED IN THIS SET ARE TYPICAL, CONSULT WITH YOUR BUILDER FOR DETAILS THAT MEETS YOUR LOCAL BUILDING CODE.
3. MATERIALS AND FINISHES ILLUSTRATED IN THIS SET ARE TYPICAL, AND SHOULD BE VERIFIED BY YOUR BUILDER OR DESIGNER BEFORE CONSTRUCTION.
4. THIS DRAWING SET IS NOT INTENDED FOR PERMITTING OR CONSTRUCTION. CONSULT WITH YOUR LOCAL BUILDING DEPARTMENT FOR BUILDING CODE REQUIREMENTS.

No.	Description	Date

22x36 A-FRAME CABIN

EAST & WEST ELEVATION

Project number	DC-003
Date	
Drawn by	T.H
Checked by	E.S

B-105

Sheet Number	
Scale	3/16" = 1'-0"

Copyrighted @DIYWEEKEND

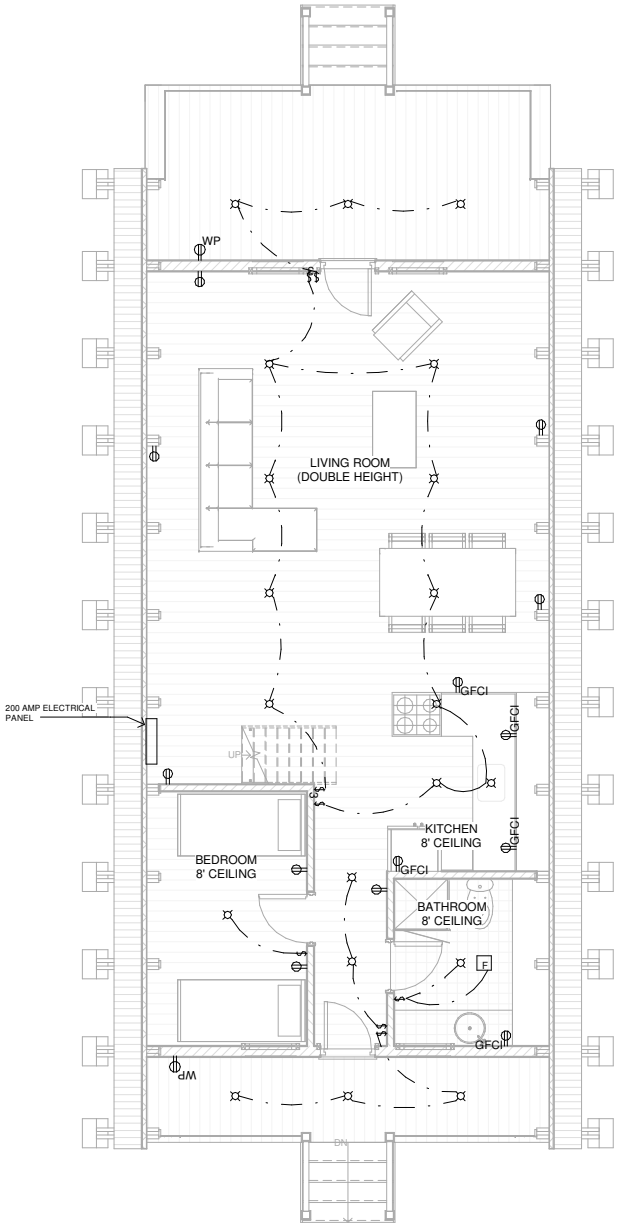

ELECTRICAL PLAN
GROUND LEVEL
SCALE: 1/4"=1' - 0"

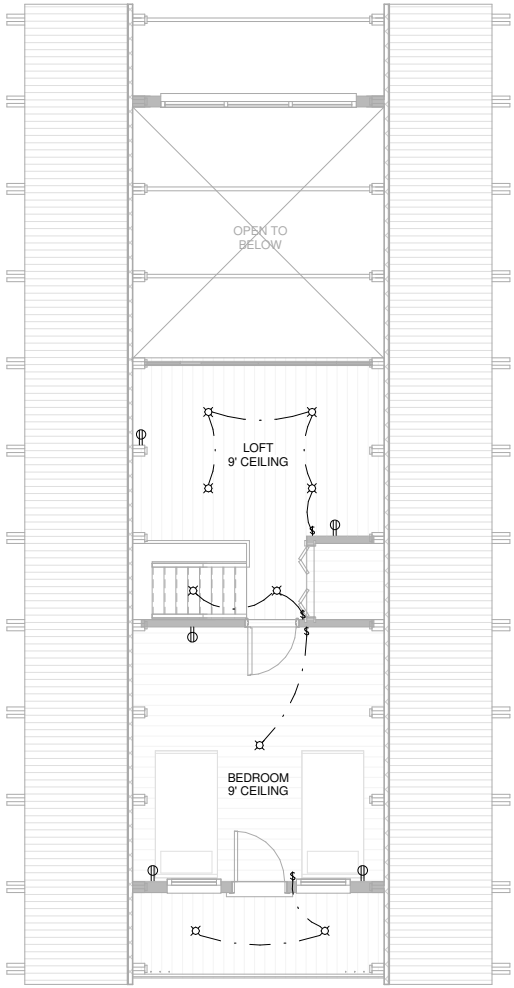

ELECTRICAL PLAN
SECOND LEVEL
SCALE: 1/4"=1' - 0"

NOTES

1. DRAWINGS SHOULD BE PRINTED ON ANSI C SIZE PAPER TO ENSURE ACCURATE SCALE PRINTING 1/4" = 1'-0"
2. CONSTRUCTION DETAILS ILLUSTRATED IN THIS SET ARE TYPICAL, CONSULT WITH YOUR BUILDER FOR DETAILS THAT MEETS YOUR LOCAL BUILDING CODE.
3. MATERIALS AND FINISHES ILLUSTRATED IN THIS SET ARE TYPICAL, AND SHOULD BE VERIFIED BY YOUR BUILDER OR DESIGNER BEFORE CONSTRUCTION.
4. THIS DRAWING SET IS NOT INTENDED FOR PERMITTING OR CONSTRUCTION. CONSULT WITH YOUR LOCAL BUILDING DEPARTMENT FOR BUILDING CODE REQUIREMENTS.

No.	Description	Date

22x36 A-FRAME CABIN

ELECTRICAL PLAN

Project number	**DC-003**
Date	
Drawn by	T.H
Checked by	E.S

B-106

Sheet Number	
Scale	**1/4" = 1'-0"**

Copyrighted @DIYWEEKEND

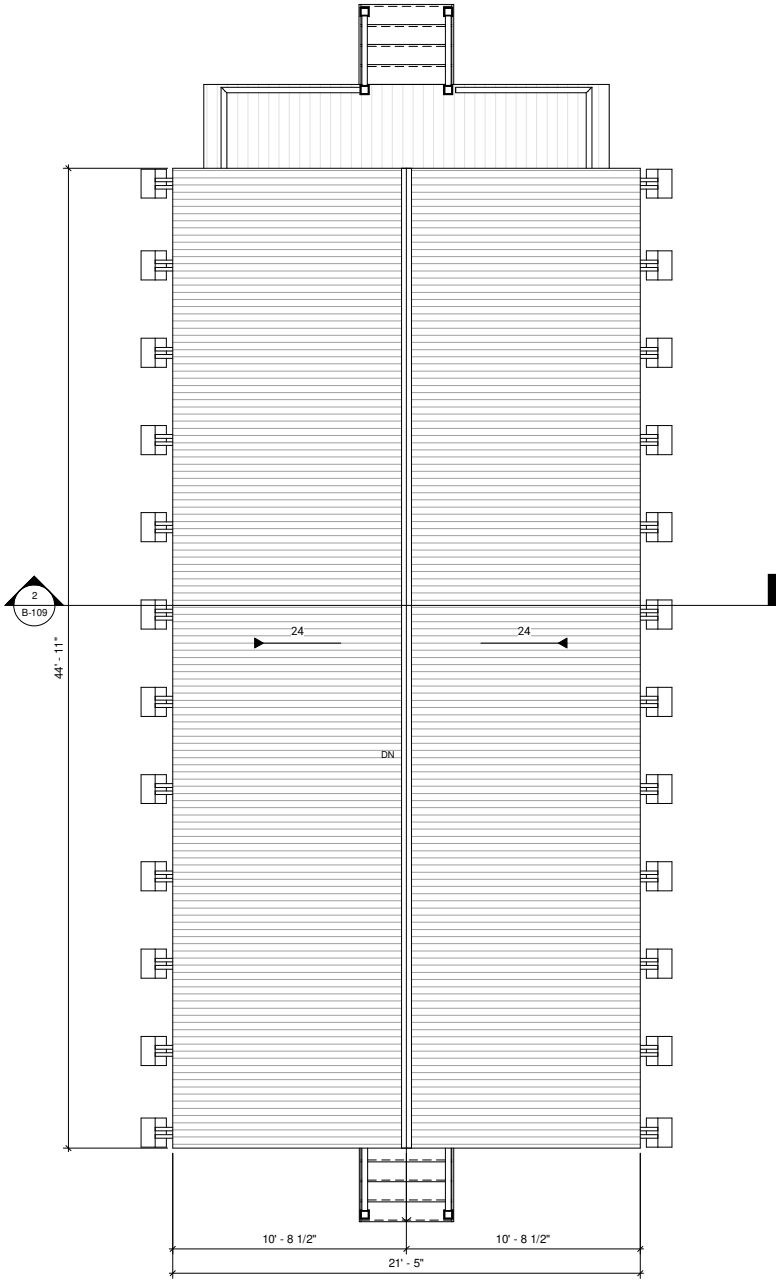

ROOF PLAN

SCALE = 1/4" : 1' - 0"

NOTES

1. DRAWINGS SHOULD BE PRINTED ON ANSI C SIZE PAPER TO ENSURE ACCURATE SCALE PRINTING 1/4" = 1'-0"
2. CONSTRUCTION DETAILS ILLUSTRATED IN THIS SET ARE TYPICAL, CONSULT WITH YOUR BUILDER FOR DETAILS THAT MEETS YOUR LOCAL BUILDING CODE.
3. MATERIALS AND FINISHES ILLUSTRATED IN THIS SET ARE TYPICAL, AND SHOULD BE VERIFIED BY YOUR BUILDER OR DESIGNER BEFORE CONSTRUCTION.
4. THIS DRAWING SET IS NOT INTENDED FOR PERMITTING OR CONSTRUCTION. CONSULT WITH YOUR LOCAL BUILDING DEPARTMENT FOR BUILDING CODE REQUIREMENTS.

No.	Description	Date

22x36 A-FRAME CABIN

ROOF PLAN

Project number	**DC-003**
Date	
Drawn by	T.H
Checked by	E.S

B-107

Sheet Number	
Scale	**1/4" = 1'-0"**

Copyrighted @DIYWEEKEND

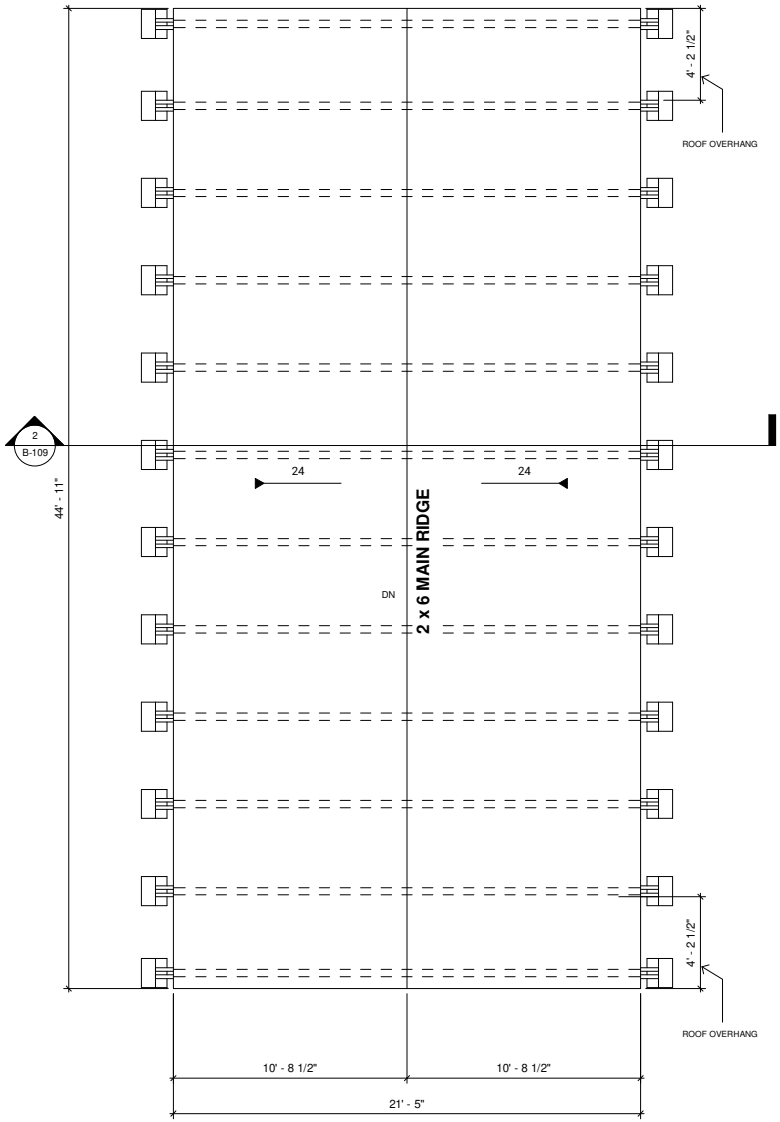

ROOF FRAMING PLAN

SCALE = 1/4" : 1' - 0"

NOTES

1. DRAWINGS SHOULD BE PRINTED ON ANSI C SIZE PAPER TO ENSURE ACCURATE SCALE PRINTING 1/4" = 1'-0"
2. CONSTRUCTION DETAILS ILLUSTRATED IN THIS SET ARE TYPICAL, CONSULT WITH YOUR BUILDER FOR DETAILS THAT MEETS YOUR LOCAL BUILDING CODE.
3. MATERIALS AND FINISHES ILLUSTRATED IN THIS SET ARE TYPICAL, AND SHOULD BE VERIFIED BY YOUR BUILDER OR DESIGNER BEFORE CONSTRUCTION.
4. THIS DRAWING SET IS NOT INTENDED FOR PERMITTING OR CONSTRUCTION. CONSULT WITH YOUR LOCAL BUILDING DEPARTMENT FOR BUILDING CODE REQUIREMENTS.

No.	Description	Date

22x36 A-FRAME CABIN

ROOF FRAMING PLAN

Project number	**DC-003**
Date	
Drawn by	T.H
Checked by	E.S

B-108

Sheet Number	
Scale	**1/4" = 1'-0"**

Copyrighted @DIYWEEKEND

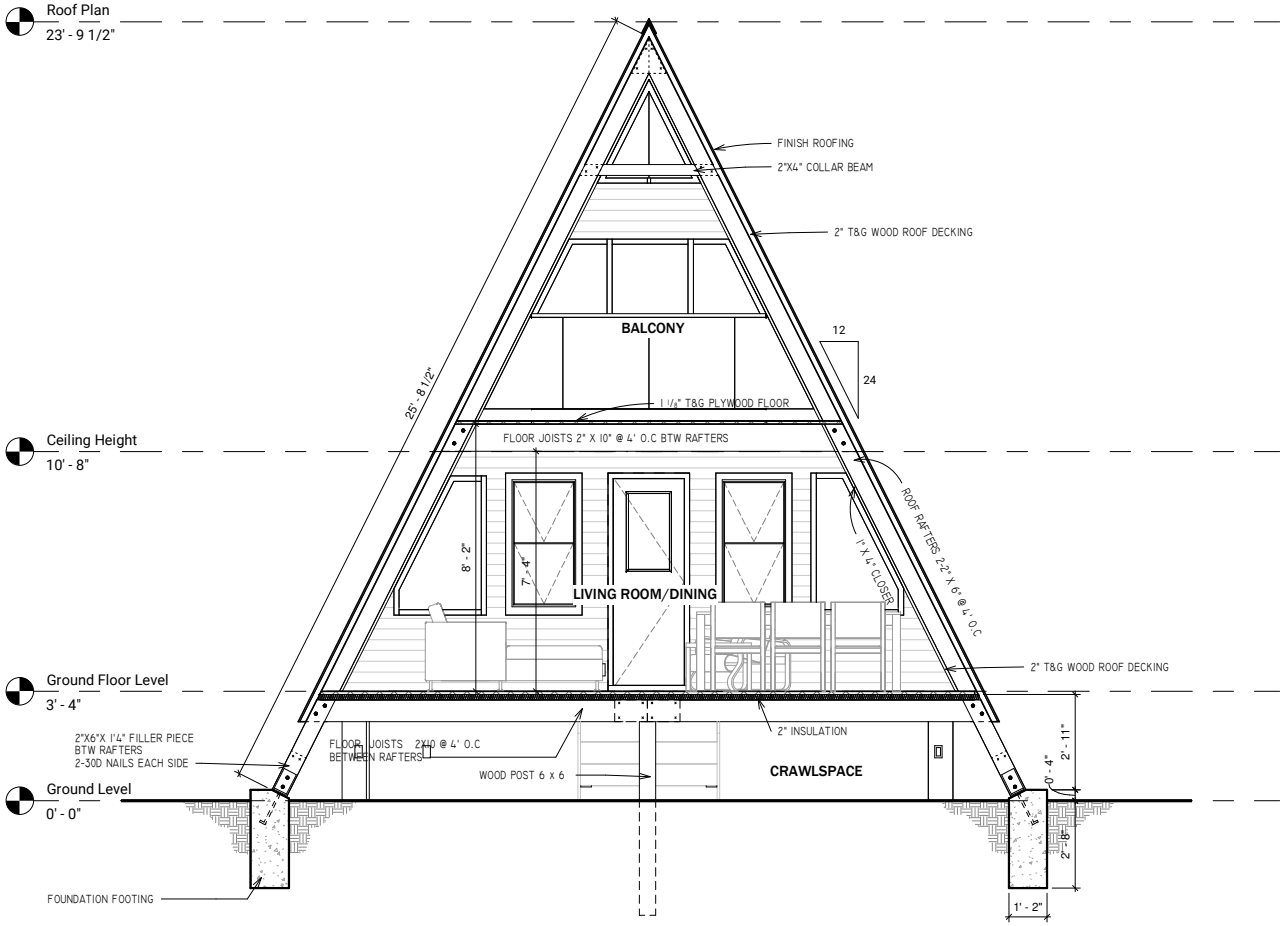

SECTION DETAIL 1

SCALE = 3/8" : 1' - 0"

NOTES

1. DRAWINGS SHOULD BE PRINTED ON ANSI C SIZE PAPER TO ENSURE ACCURATE SCALE PRINTING 3/8" = 1'-0"
2. CONSTRUCTION DETAILS ILLUSTRATED IN THIS SET ARE TYPICAL, CONSULT WITH YOUR BUILDER FOR DETAILS THAT MEETS YOUR LOCAL BUILDING CODE.
3. MATERIALS AND FINISHES ILLUSTRATED IN THIS SET ARE TYPICAL, AND SHOULD BE VERIFIED BY YOUR BUILDER OR DESIGNER BEFORE CONSTRUCTION.
4. THIS DRAWING SET IS NOT INTENDED FOR PERMITTING OR CONSTRUCTION. CONSULT WITH YOUR LOCAL BUILDING DEPARTMENT FOR BUILDING CODE REQUIREMENTS.

No.	Description	Date

22x36 A-FRAME CABIN

SECTION DETAIL

Project number	DC-003
Date	
Drawn by	T.H
Checked by	E.S

B-109

Sheet Number	
Scale	3/8" = 1'-0"

Copyrighted @DIYWEEKEND

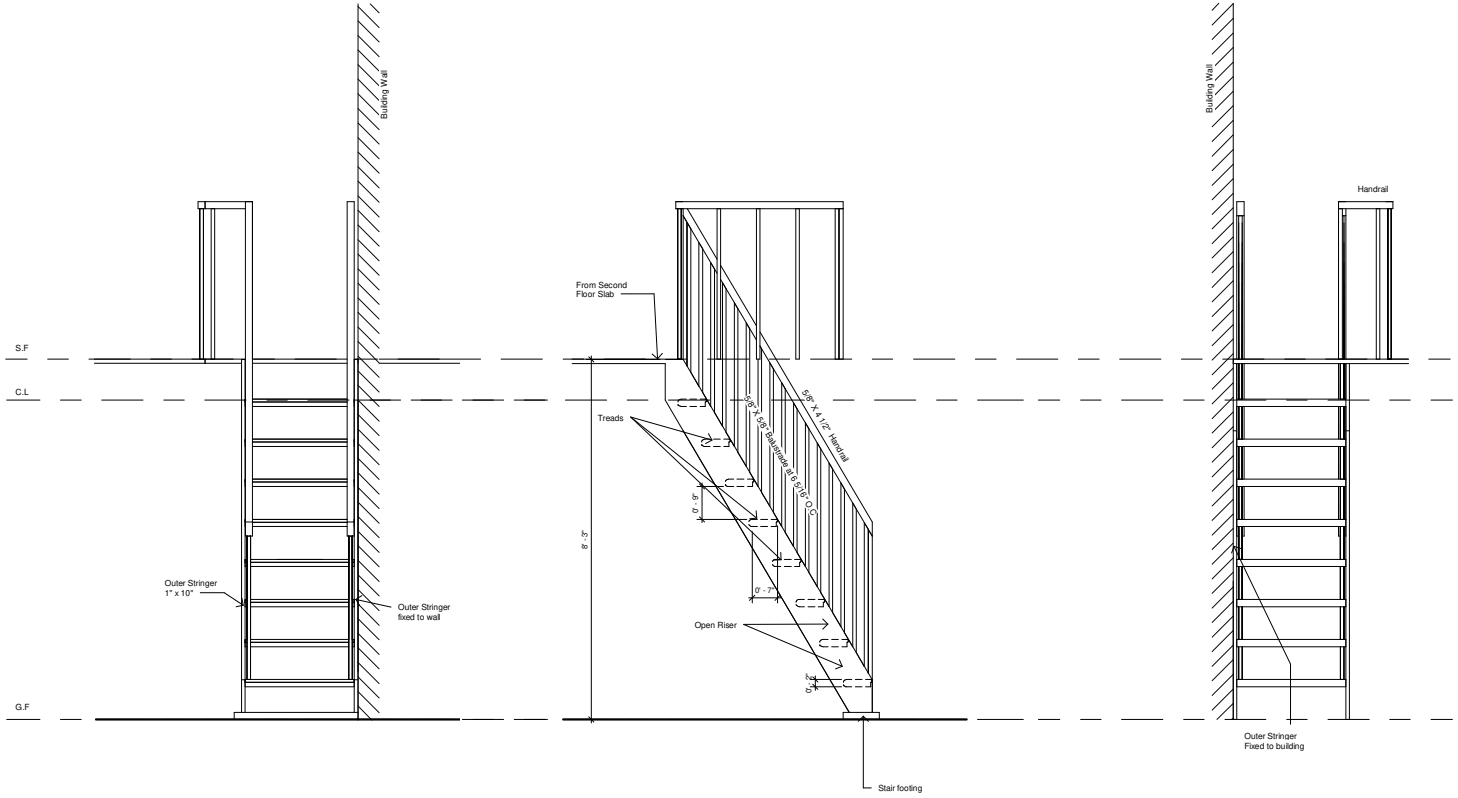

FRONT VIEW

SIDE VIEW

REAR VIEW

NOTES

1. DRAWINGS SHOULD BE PRINTED ON ANSI C SIZE PAPER TO ENSURE ACCURATE SCALE PRINTING 1/2" = 1'-0"
2. CONSTRUCTION DETAILS ILLUSTRATED IN THIS SET ARE TYPICAL, CONSULT WITH YOUR BUILDER FOR DETAILS THAT MEETS YOUR LOCAL BUILDING CODE.
3. MATERIALS AND FINISHES ILLUSTRATED IN THIS SET ARE TYPICAL, AND SHOULD BE VERIFIED BY YOUR BUILDER OR DESIGNER BEFORE CONSTRUCTION.
4. THIS DRAWING SET IS NOT INTENDED FOR PERMITTING OR CONSTRUCTION. CONSULT WITH YOUR LOCAL BUILDING DEPARTMENT FOR BUILDING CODE REQUIREMENTS.

No.	Description	Date

22x36 A-FRAME CABIN

STAIRCASE LAYOUT

Project number	**DC-003**
Date	
Drawn by	T.H
Checked by	E.S

B-110

Sheet Number	
Scale	**1/2" = 1'-0"**

Copyrighted @DIYWEEKEND

DOOR SCHEDULE

	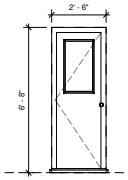	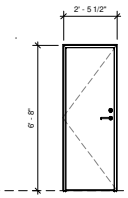	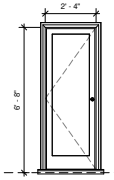	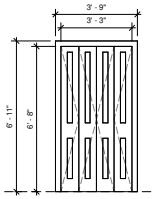	
FL					
Mark/Tag	D1	D2	D3	D4	
Quantity	2	3	1	1	
Location	Front Entrance Rear Exit (Kitchen)	Bedrooms Bath / Toilet	Balcony Front Exit	Closet	
Description	Timber Glazed panel door External Door Paint Finished	Timber Flush door Interior Door Plywood Sheath Finished	Timber Glazed Panel door Interior Door Plywood Sheath Finished	Timber Panel double bifold door Interior Door Plywood Sheath Finished	

NOTES

1. DRAWINGS SHOULD BE PRINTED ON ANSI C SIZE PAPER TO ENSURE ACCURATE SCALE PRINTING 1/4" = 1'-0"
2. CONSTRUCTION DETAILS ILLUSTRATED IN THIS SET ARE TYPICAL, CONSULT WITH YOUR BUILDER FOR DETAILS THAT MEETS YOUR LOCAL BUILDING CODE.
3. MATERIALS AND FINISHES ILLUSTRATED IN THIS SET ARE TYPICAL, AND SHOULD BE VERIFIED BY YOUR BUILDER OR DESIGNER BEFORE CONSTRUCTION.
4. THIS DRAWING SET IS NOT INTENDED FOR PERMITTING OR CONSTRUCTION. CONSULT WITH YOUR LOCAL BUILDING DEPARTMENT FOR BUILDING CODE REQUIREMENTS.

No.	Description	Date

22x36 A-FRAME CABIN

DOOR SCHEDULES

Project number	**DC-003**
Date	
Drawn by	T.H
Checked by	E.S

C-101

Sheet Number	
Scale	**1/4" = 1'-0"**

Copyrighted @DIYWEEKEND

WINDOWS SCHEDULE

FL	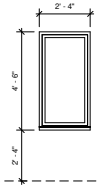	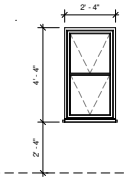	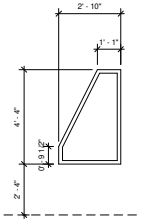	CL 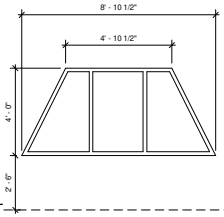	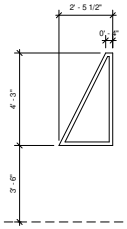
Mark/Tag	W1	W2	W3	W4	W5
Quantity	2	4	2 (Laterally mirrored)	1	1
Location	North Facade	Living Room, South facade Bath Window	Living Room North facade	Living Room Clerestory	Bedroom Window
Description	Single Fixed Window Double glazed Wood frame	Double Hung Window Double glazed Wood frame	Single Fixed Window Double glazed Wood frame	3 x 1 Fixed Window Double glazed Wood frame	Fixed Window Double glazed Wood frame

CL	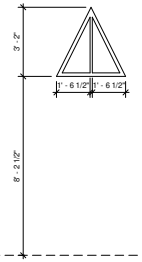				
Mark/Tag	W6				
Quantity	2				
Location	Gable Vent WIndow				
Description	2 x 1 Fixed Window Double glazed Wood frame				

NOTES

1. DRAWINGS SHOULD BE PRINTED ON ANSI C SIZE PAPER TO ENSURE ACCURATE SCALE PRINTING 1/4" = 1'-0"
2. CONSTRUCTION DETAILS ILLUSTRATED IN THIS SET ARE TYPICAL, CONSULT WITH YOUR BUILDER FOR DETAILS THAT MEETS YOUR LOCAL BUILDING CODE.
3. MATERIALS AND FINISHES ILLUSTRATED IN THIS SET ARE TYPICAL, AND SHOULD BE VERIFIED BY YOUR BUILDER OR DESIGNER BEFORE CONSTRUCTION.
4. THIS DRAWING SET IS NOT INTENDED FOR PERMITTING OR CONSTRUCTION. CONSULT WITH YOUR LOCAL BUILDING DEPARTMENT FOR BUILDING CODE REQUIREMENTS.

No.	Description	Date

22x36 A-FRAME CABIN

WINDOW SCHEDULE

Project number	**DC-003**
Date	
Drawn by	T.H
Checked by	E.S

C-102

Sheet Number	
Scale	**1/4" = 1'-0"**

Copyrighted @DIYWEEKEND